PROJET DE CONSTRUCTION D'UNE INDUSTRIE A COYAH







PAPEL INDUSTRIES

DESCRIPTIF DU PROJET

PROJET DE CONSTRUCTION D'UNE INDUSTRIE A COYAH

Surface du site: 4763.63 m²

Surface du bati: 1938.81 m²

Maitre d'ouvrage: PAPEL INDUSTRIES

Maitre d'oeuvre: BETCOM-AI

'25



'25




'25



'25


BETCOM AI
ARCHITECTURE · CONSTRUCTION · DEVELOPPEMENT

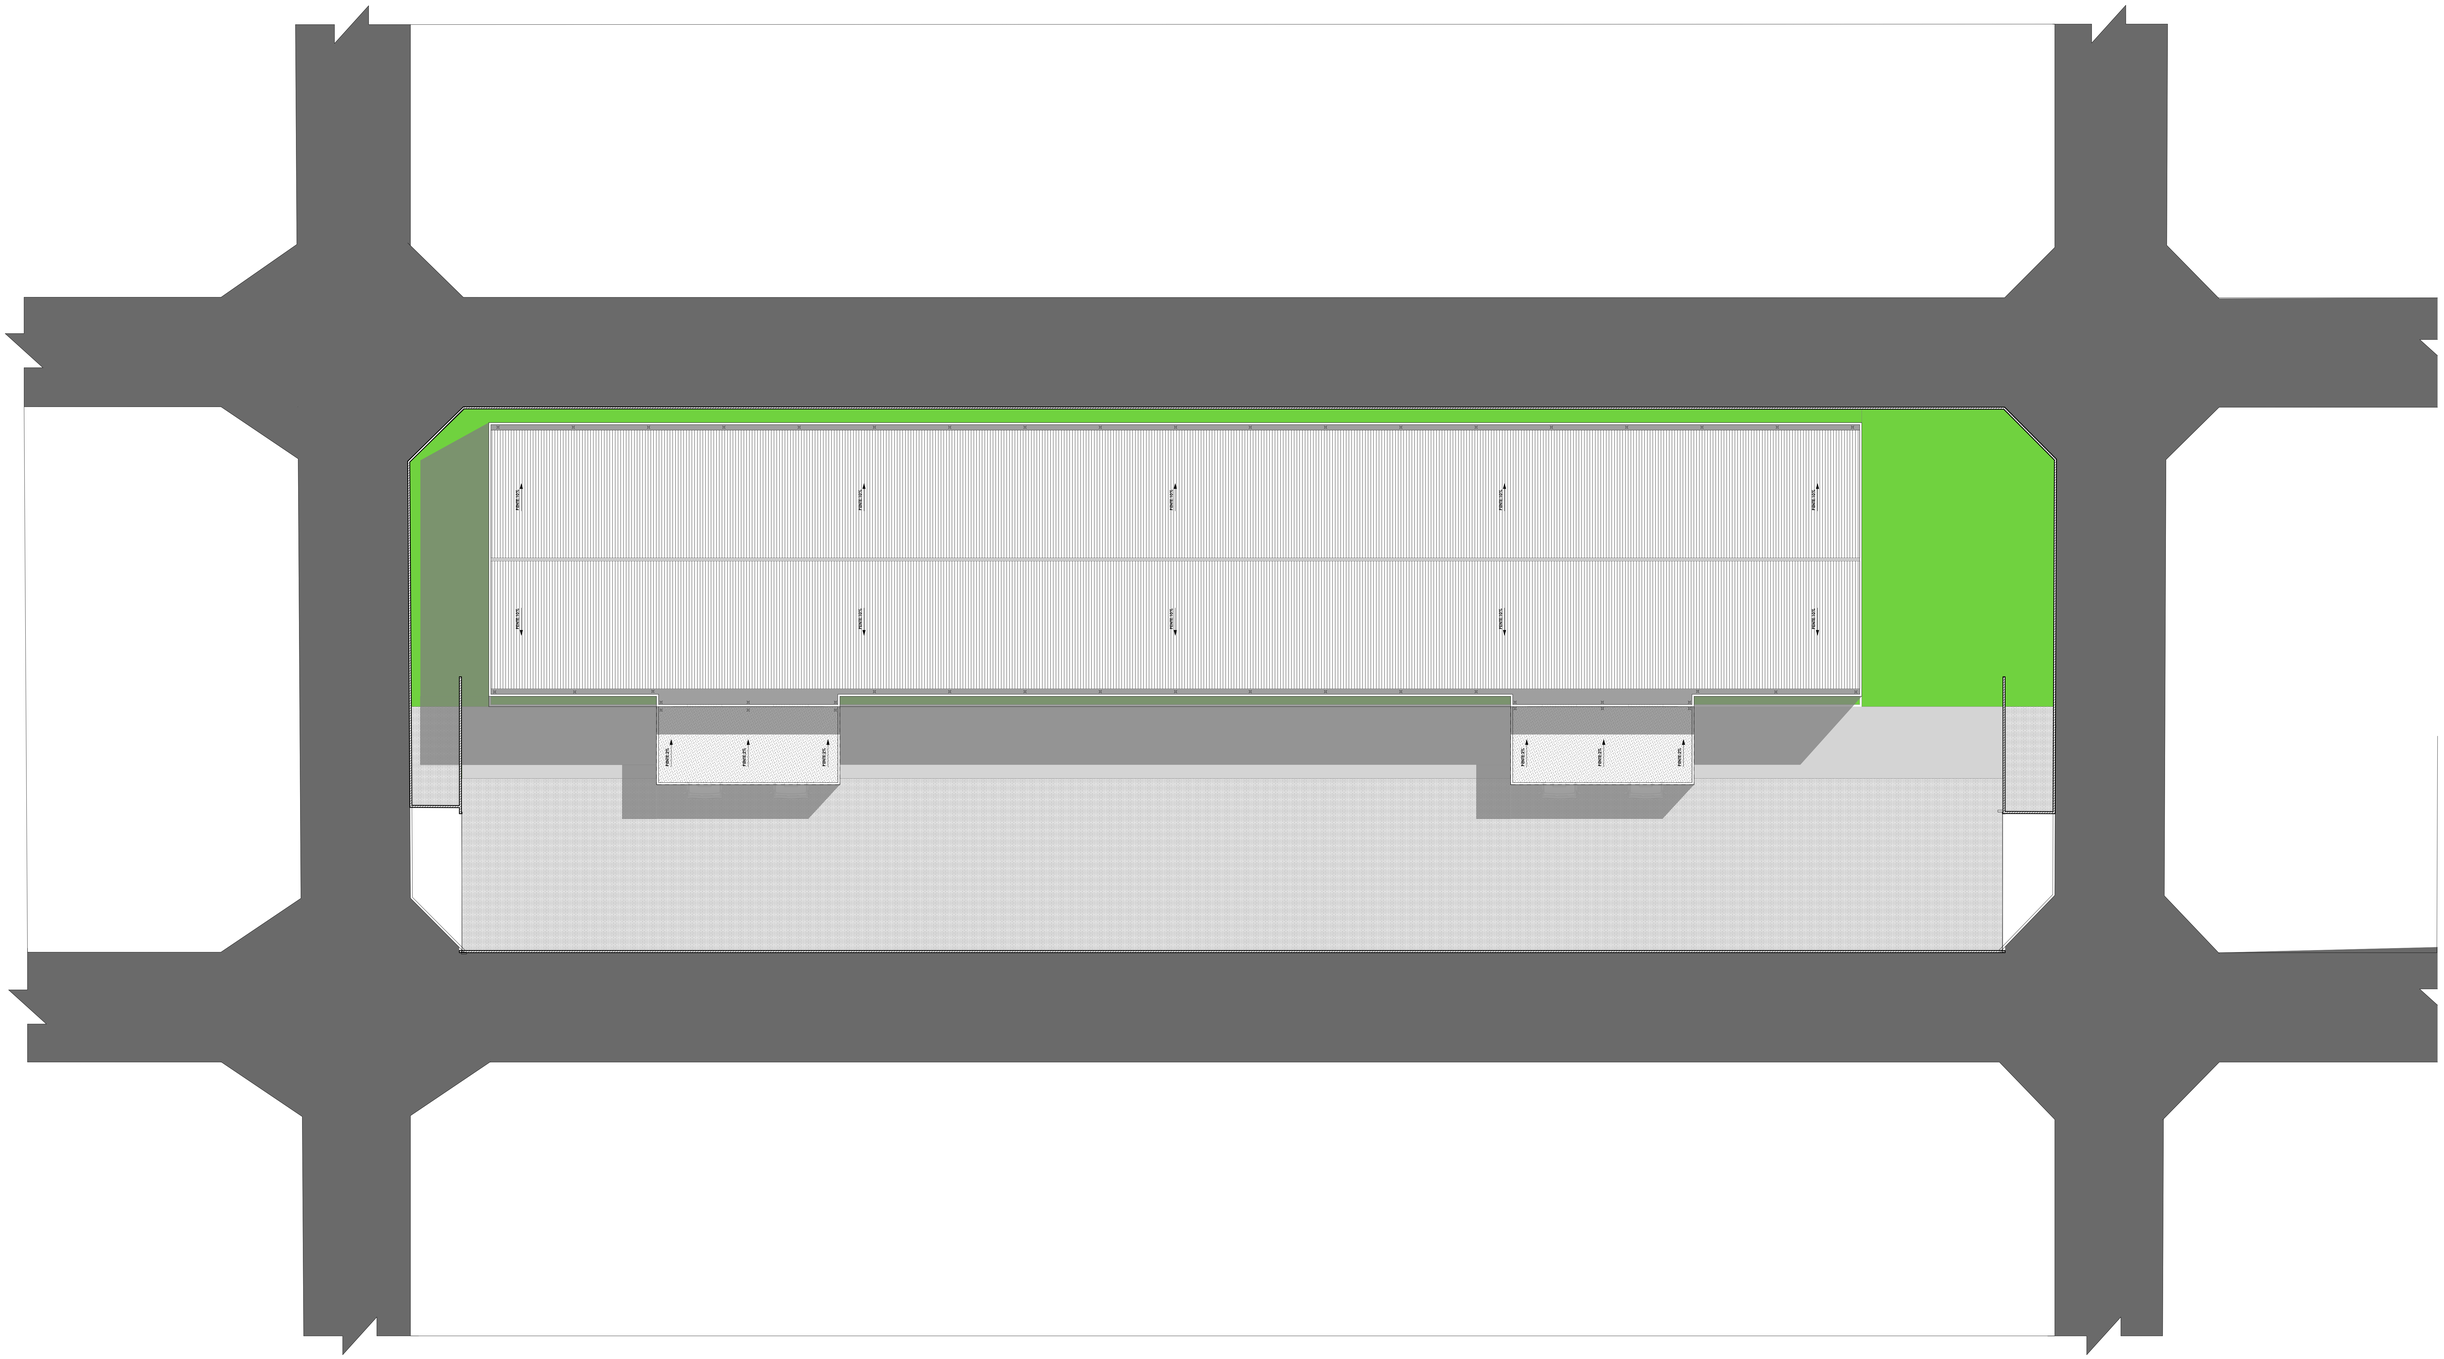

PROJET DE CONSTRUCTION D'UNE INDUSTRIE A COYAH
MAITRE D'OUVRAGE: PAPEL INDUSTRIES
MAITRE D'OEUVRE: BETCON AI
CONTACT: 625 728 627


PLAN DE MASSE
DATE:19/12/25
ECHELLE :1/100
FORMAT :A0

BETCOM AI
ARCHITECTURE · CONSTRUCTION · DEVELOPPEMENT

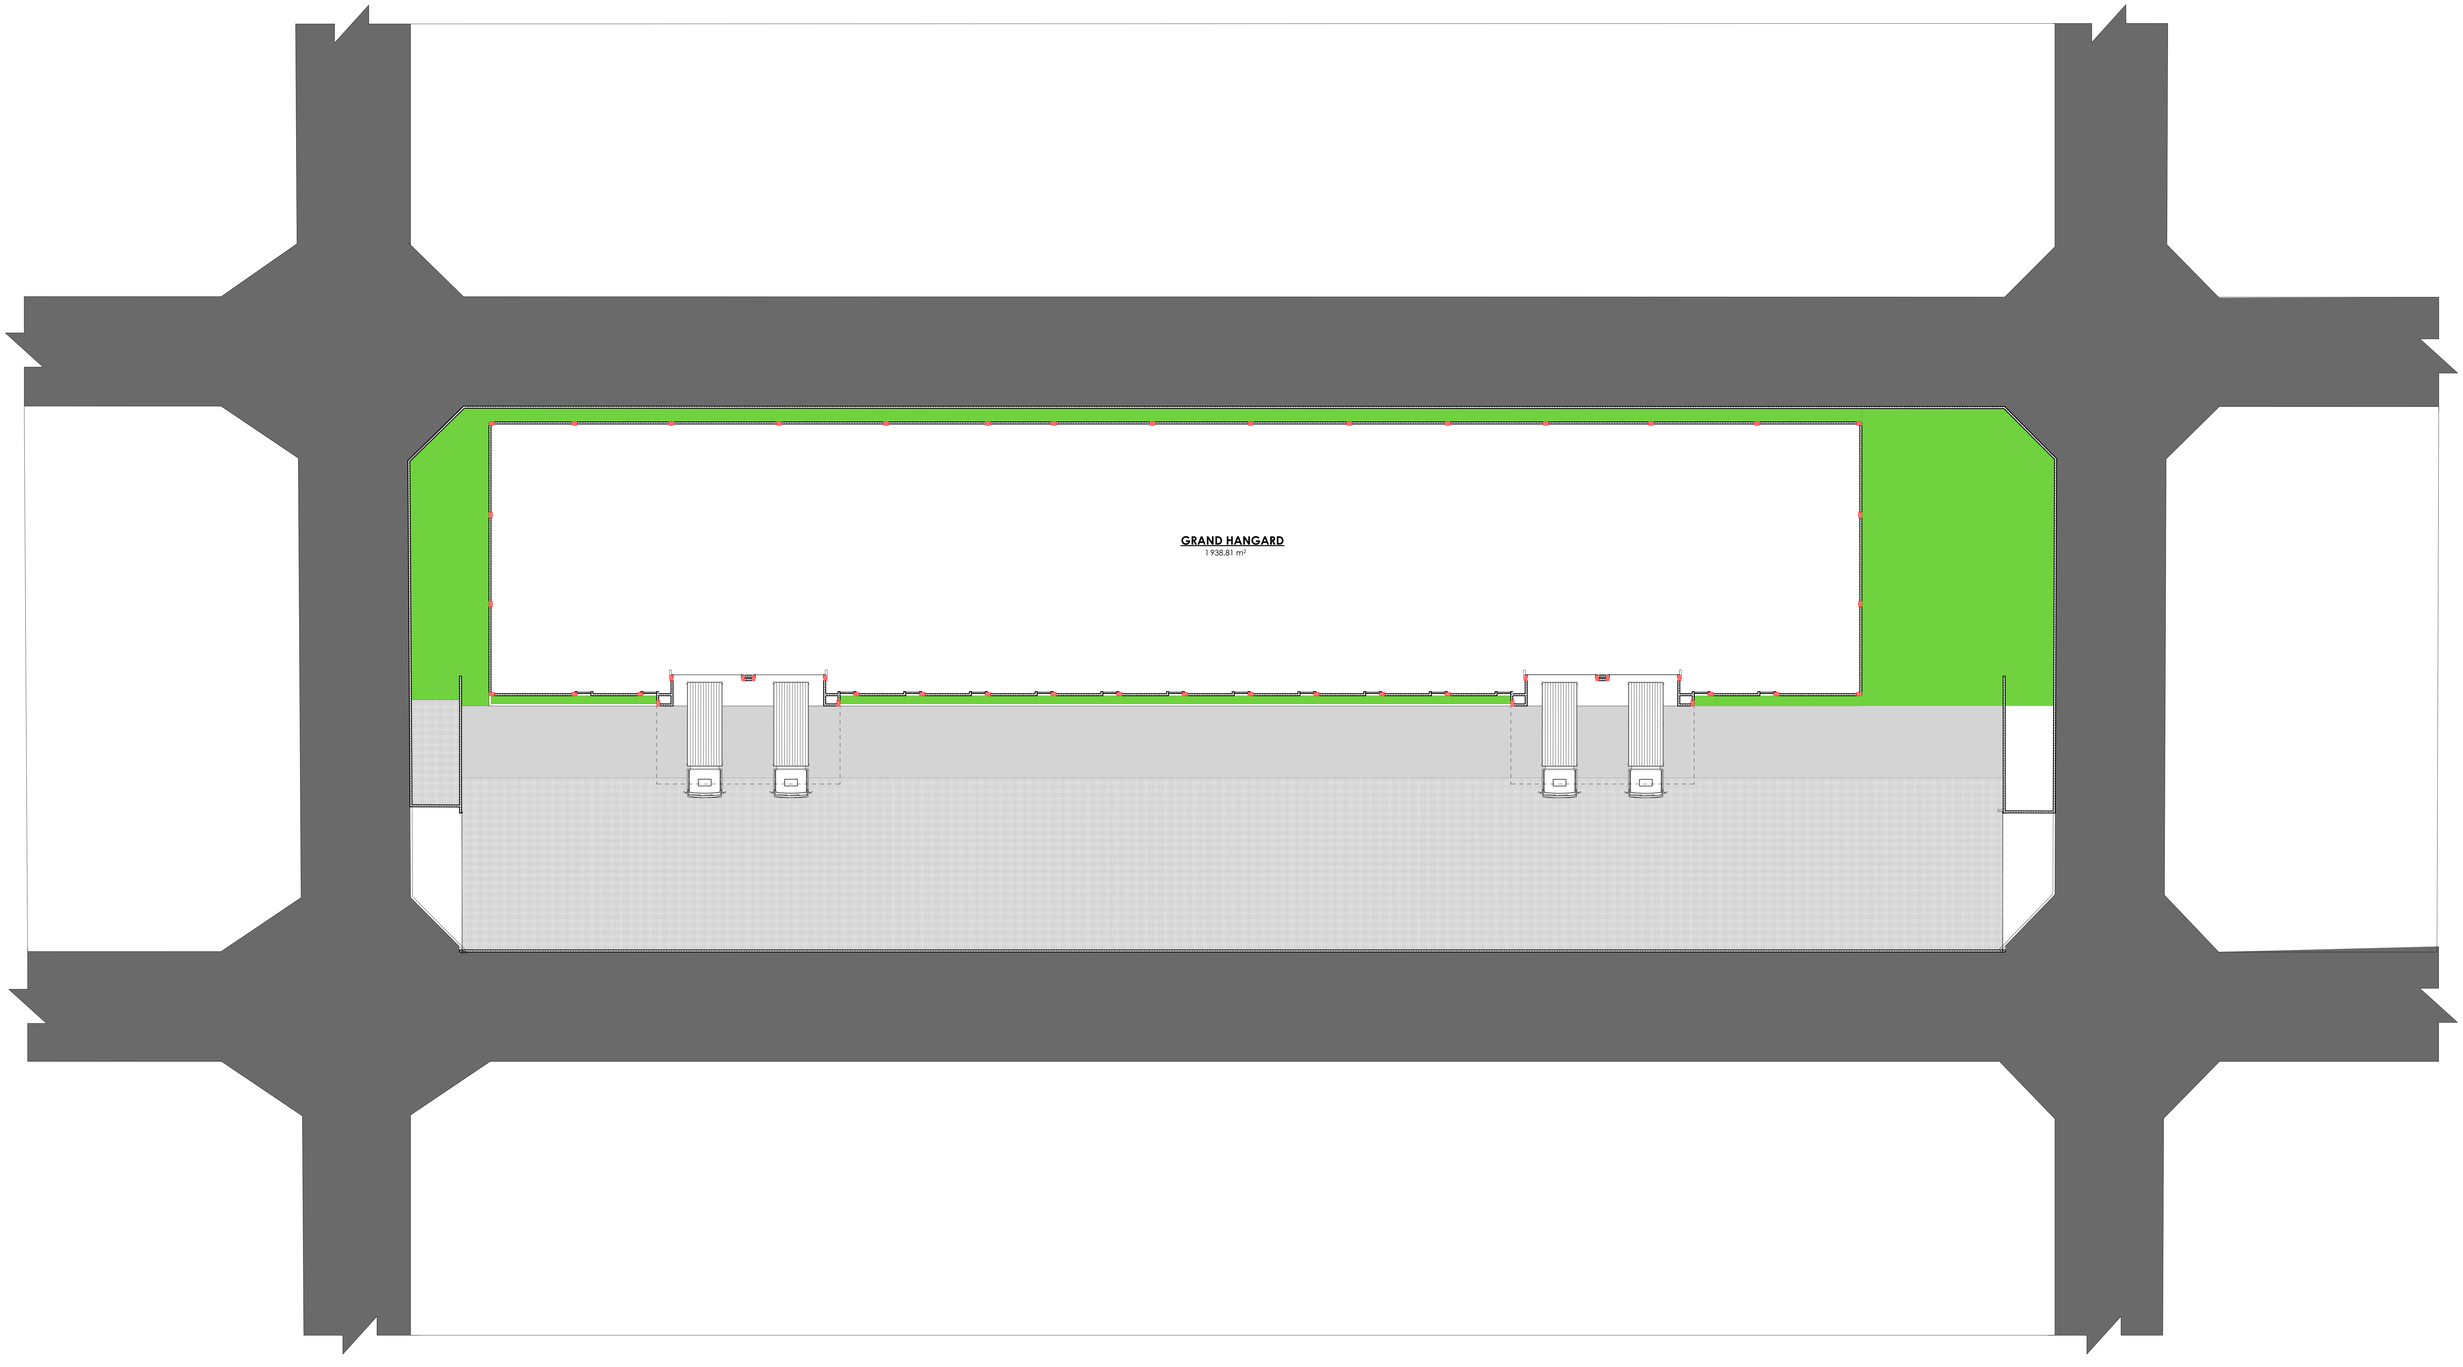

PROJET DE CONSTRUCTION D'UNE INDUSTRIE A COYAH
MAITRE D'OUVRAGE: PAPEL INDUSTRIES
MAITRE D'OEUVRE: BETCON AI
CONTACT: 625 728 627

PLAN D'ENSEMBLE
DATE:19/12/25
ECHELLE :1/100
FORMAT :A0

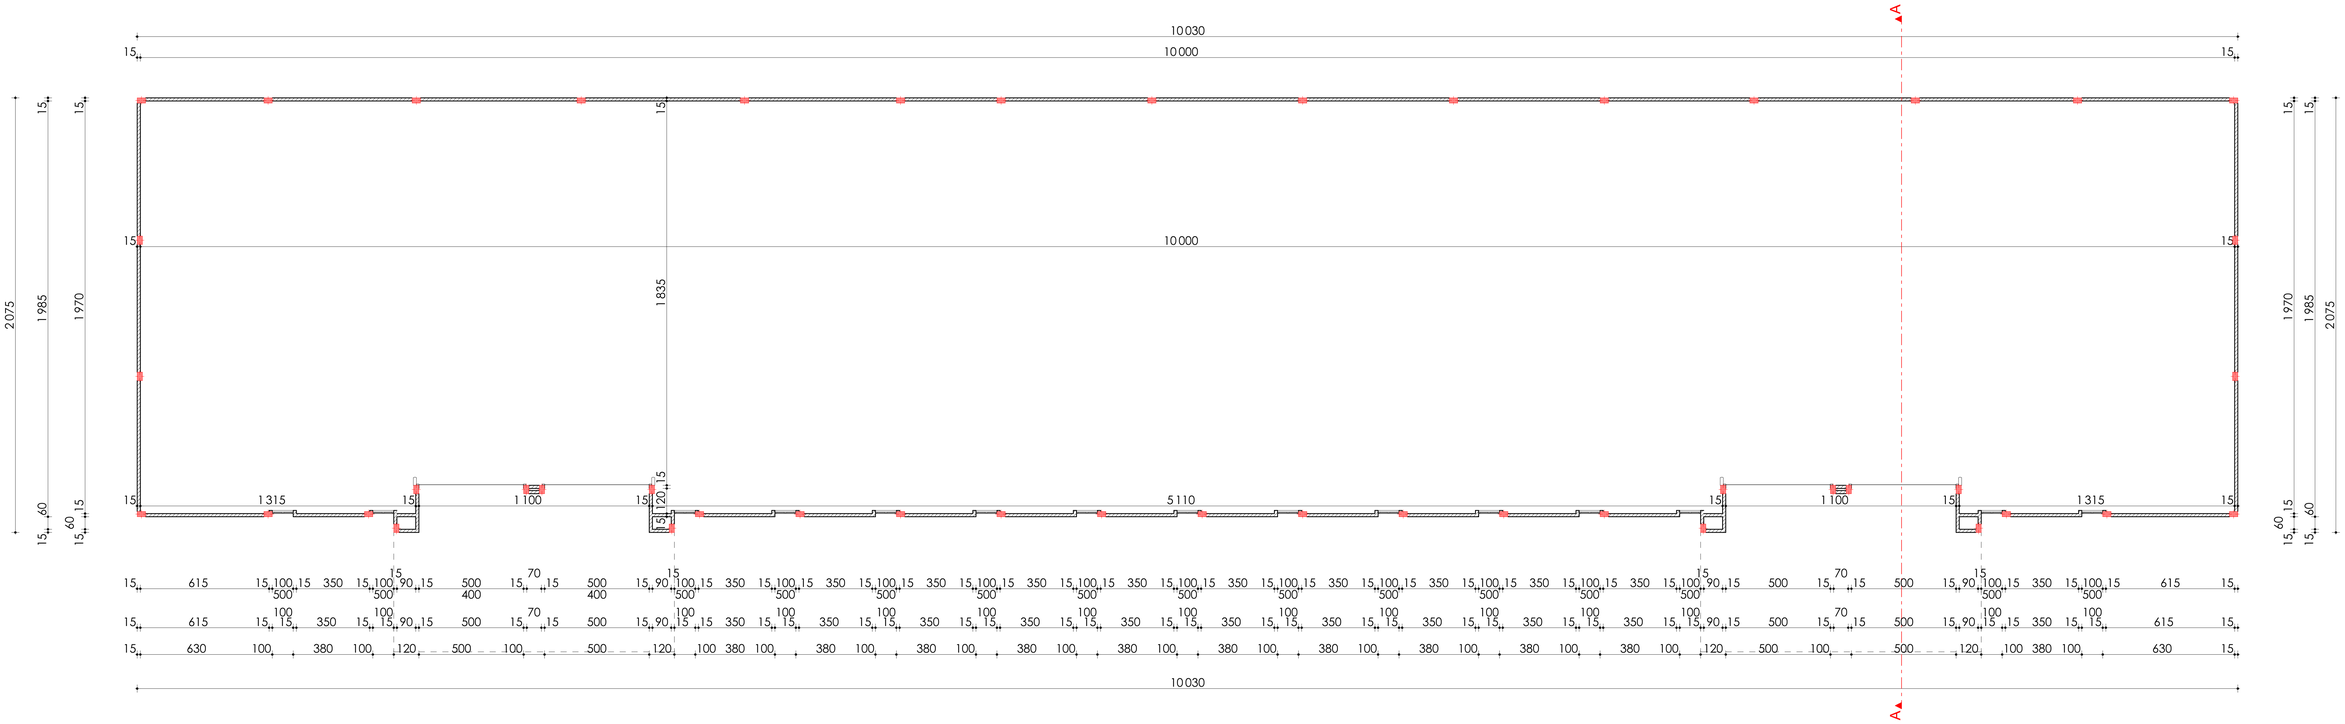

PROJET DE CONSTRUCTION D'UNE INDUSTRIE A COYAH
MAITRE D'OUVRAGE: PAPEL INDUSTRIES
MAITRE D'OEUVRE: BETCON AI
CONTACT: 625 728 627

PLAN DE COTATION
DATE:19/12/25
ECHELLE :1/100
FORMAT :A0

BETCOM AI



PROJET DE CONSTRUCTION D'UNE INDUSTRIE A COYAH

MAITRE D'OUVRAGE: PAPEL INDUSTRIES

MAITRE D'OEUVRE: BETCON AI


CONTACT: 625 728 627

PLAN DE TOITURE

DATE:19/12/25


ECHELLE :1/100


FORMAT :A0

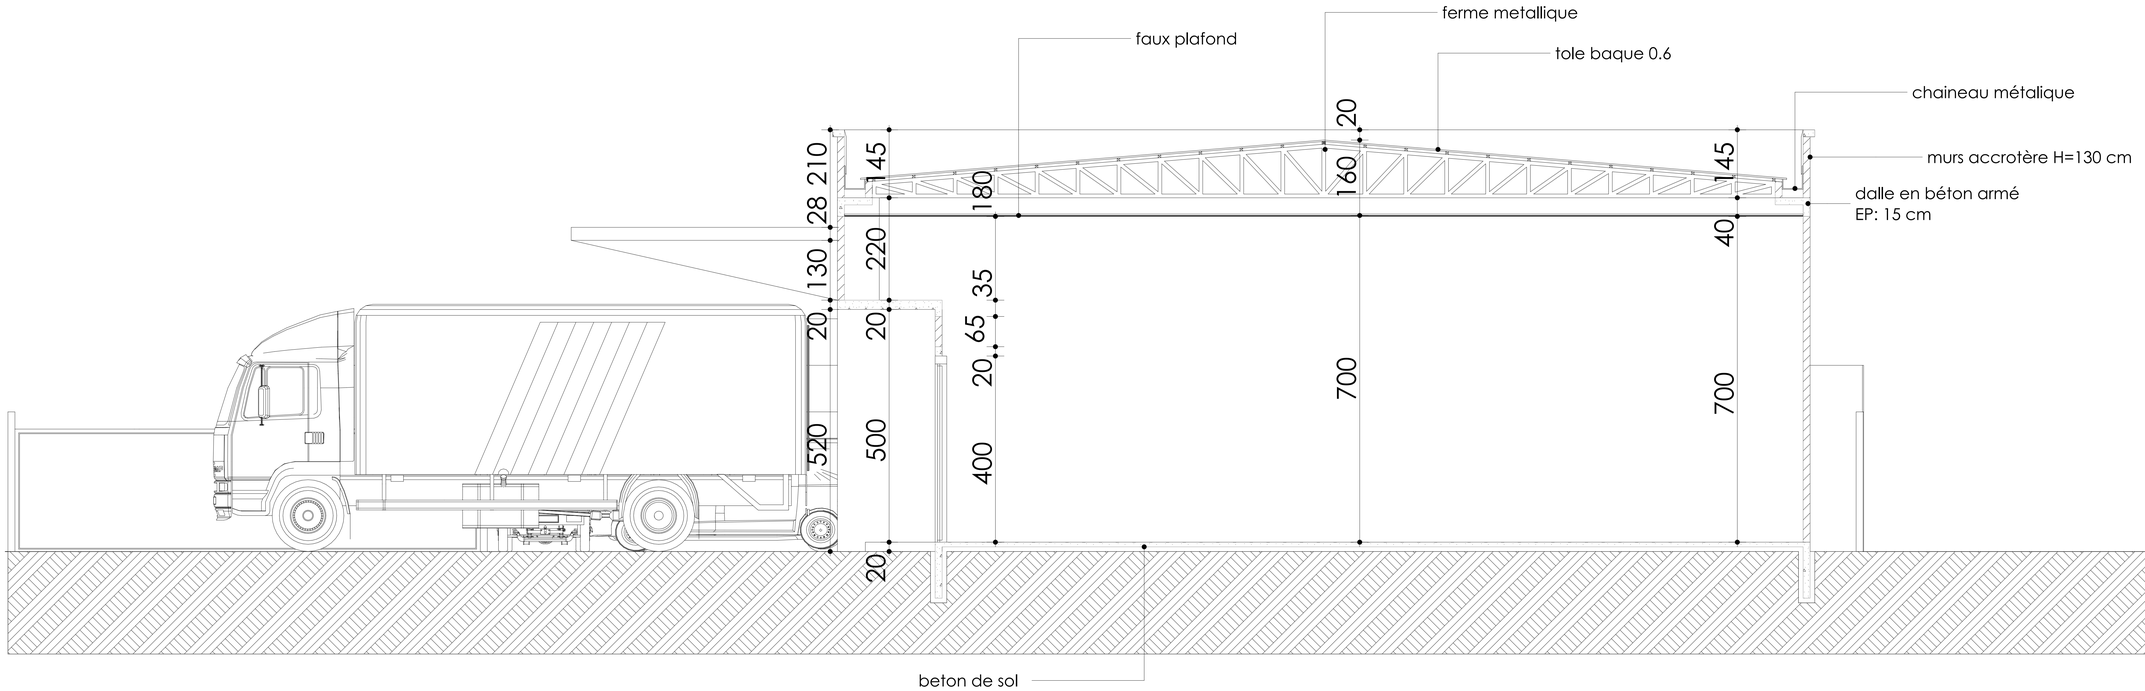

PROJET DE CONSTRUCTION D'UNE INDUSTRIE A COYAH
MAITRE D'OUVRAGE: PAPEL INDUSTRIES
MAITRE D'OEUVRE: BETCON AI
CONTACT: 625 728 627

COUPE A-A
DATE:19/12/25
ECHELLE :1/100
FORMAT :A0

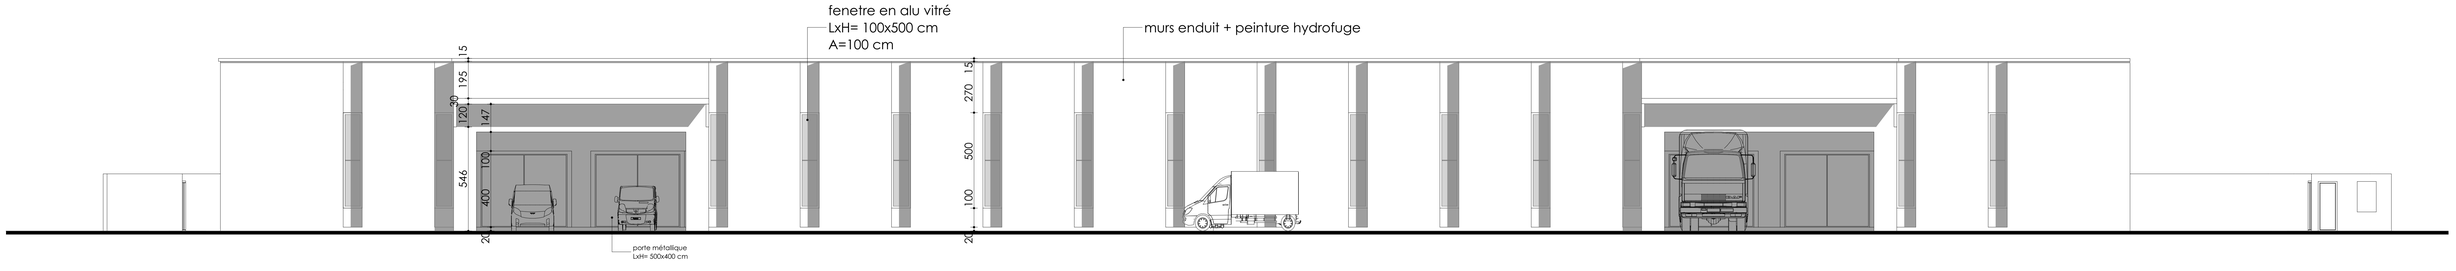

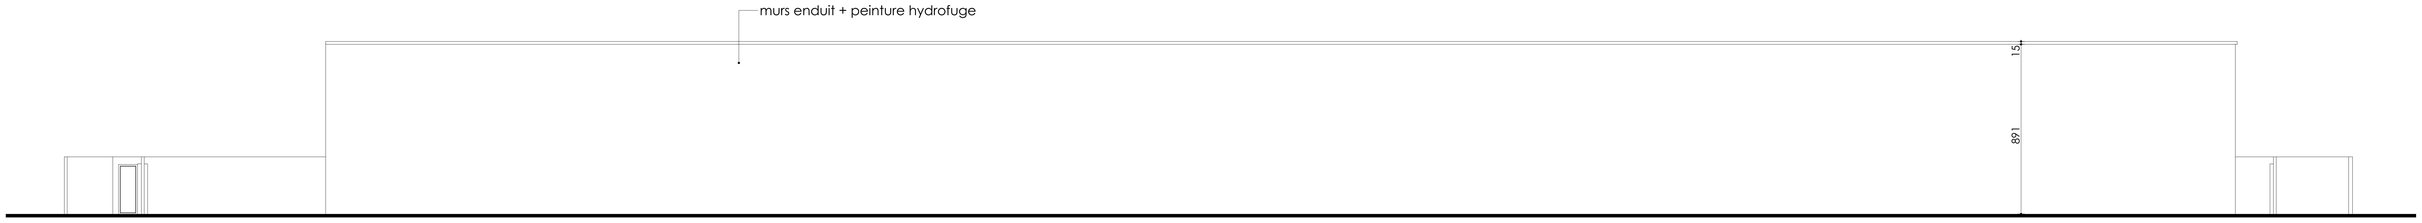

PROJET DE CONSTRUCTION D'UNE INDUSTRIE A COYAH

MAITRE D'OUVRAGE: PAPEL INDUSTRIES

MAITRE D'OEUVRE: BETCON AI


CONTACT: 625 728 627


ELEVATIONS 1-2

DATE:19/12/25

ECHELLE :1/100

FORMAT :A0

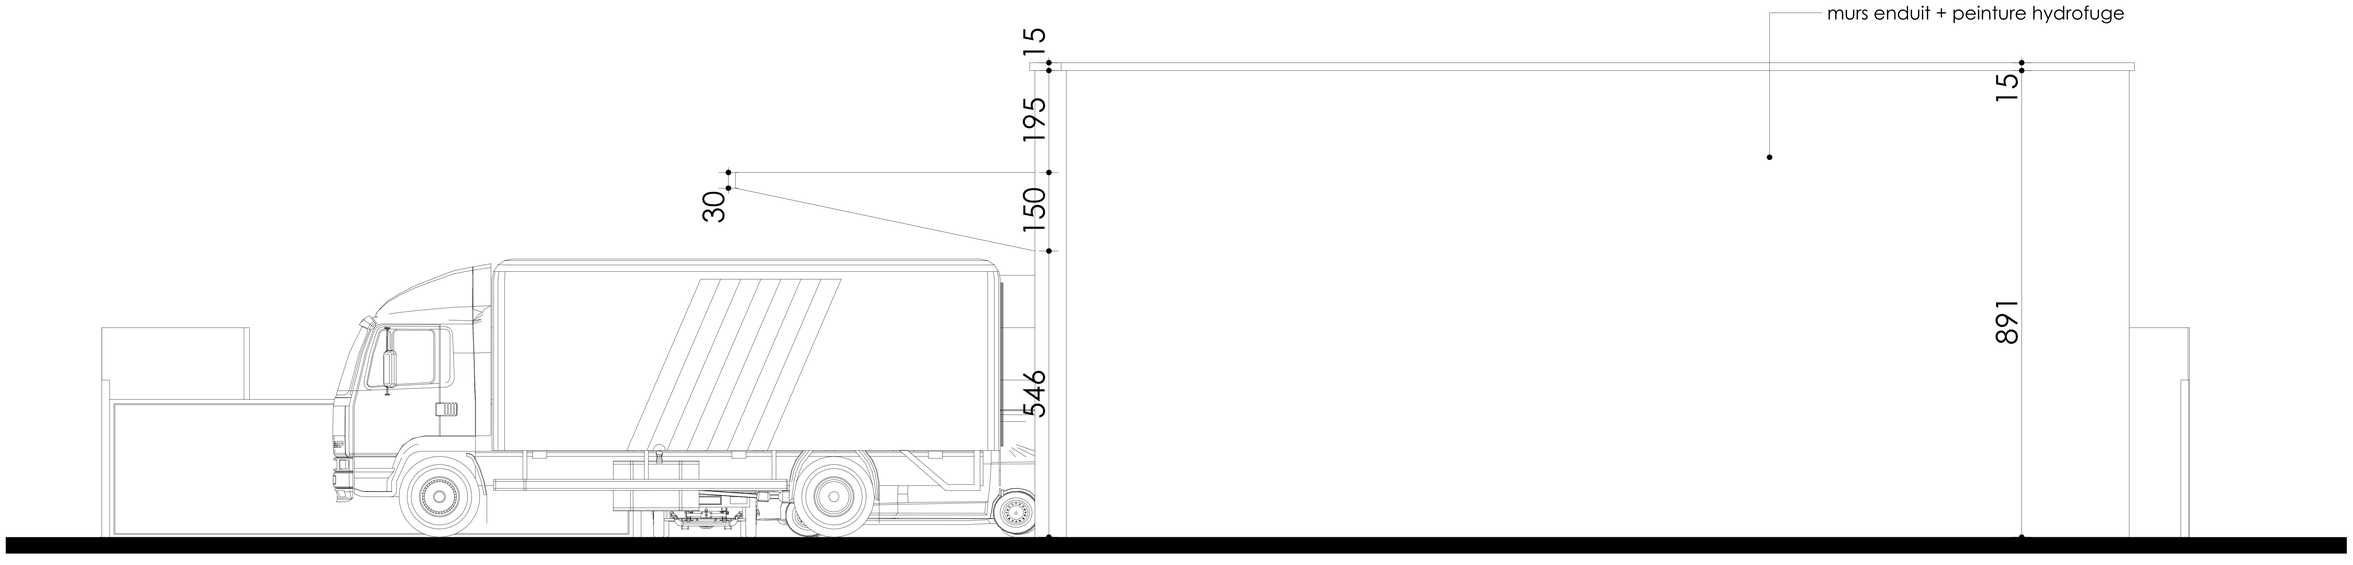

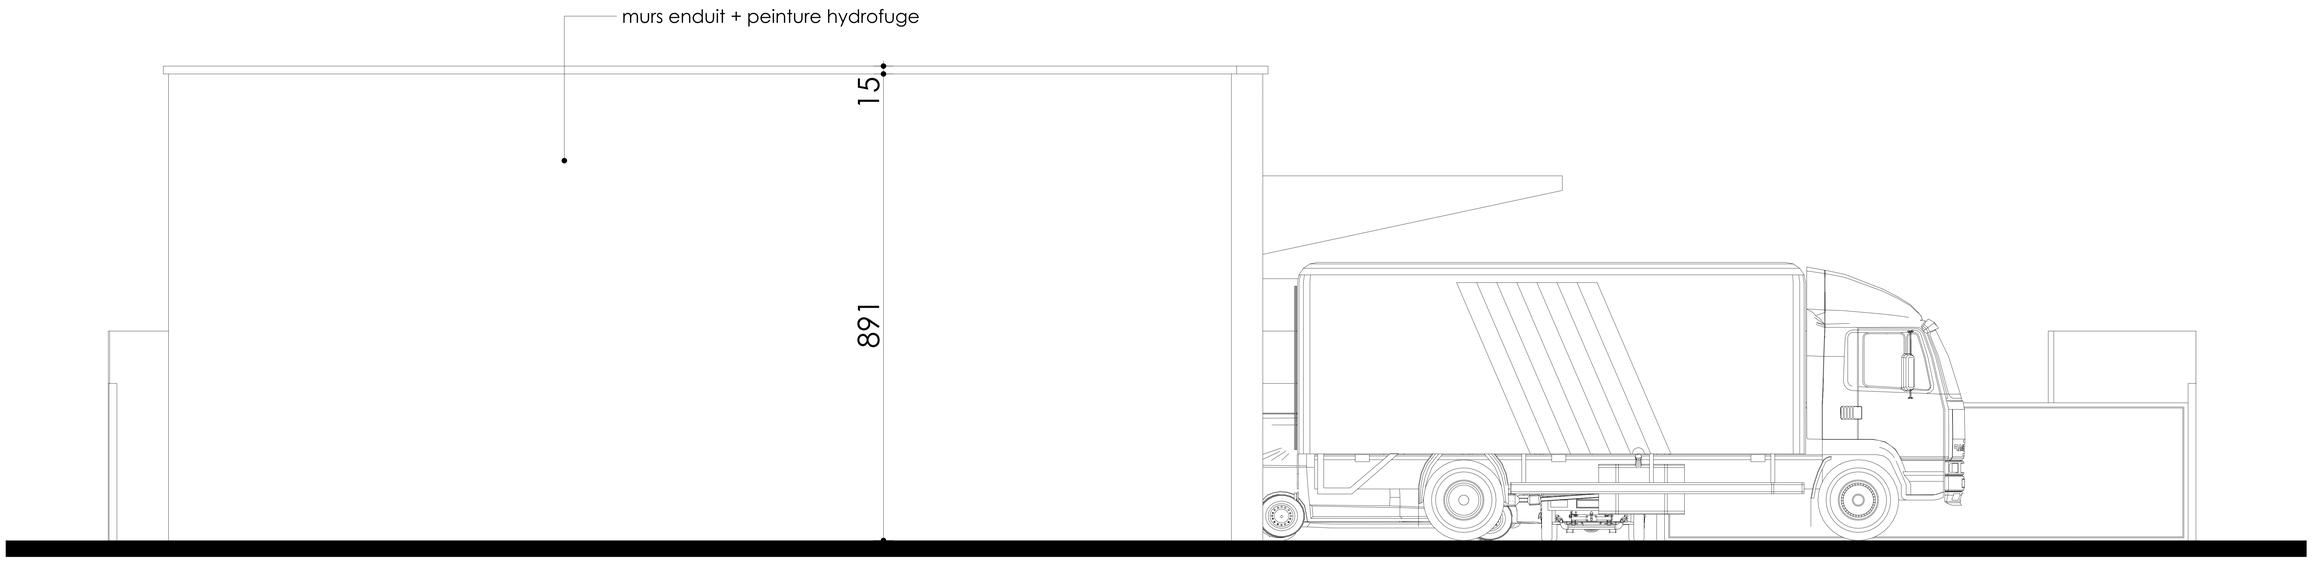

PROJET DE CONSTRUCTION D'UNE INDUSTRIE A COYAH

MAITRE D'OUVRAGE: PAPEL INDUSTRIES

MAITRE D'OEUVRE: BETCON AI

CONTACT: 625 728 627


ELEVATIONS 3-4

DATE:19/12/25

ECHELLE :1/100

FORMAT :A0

BETCOM AI

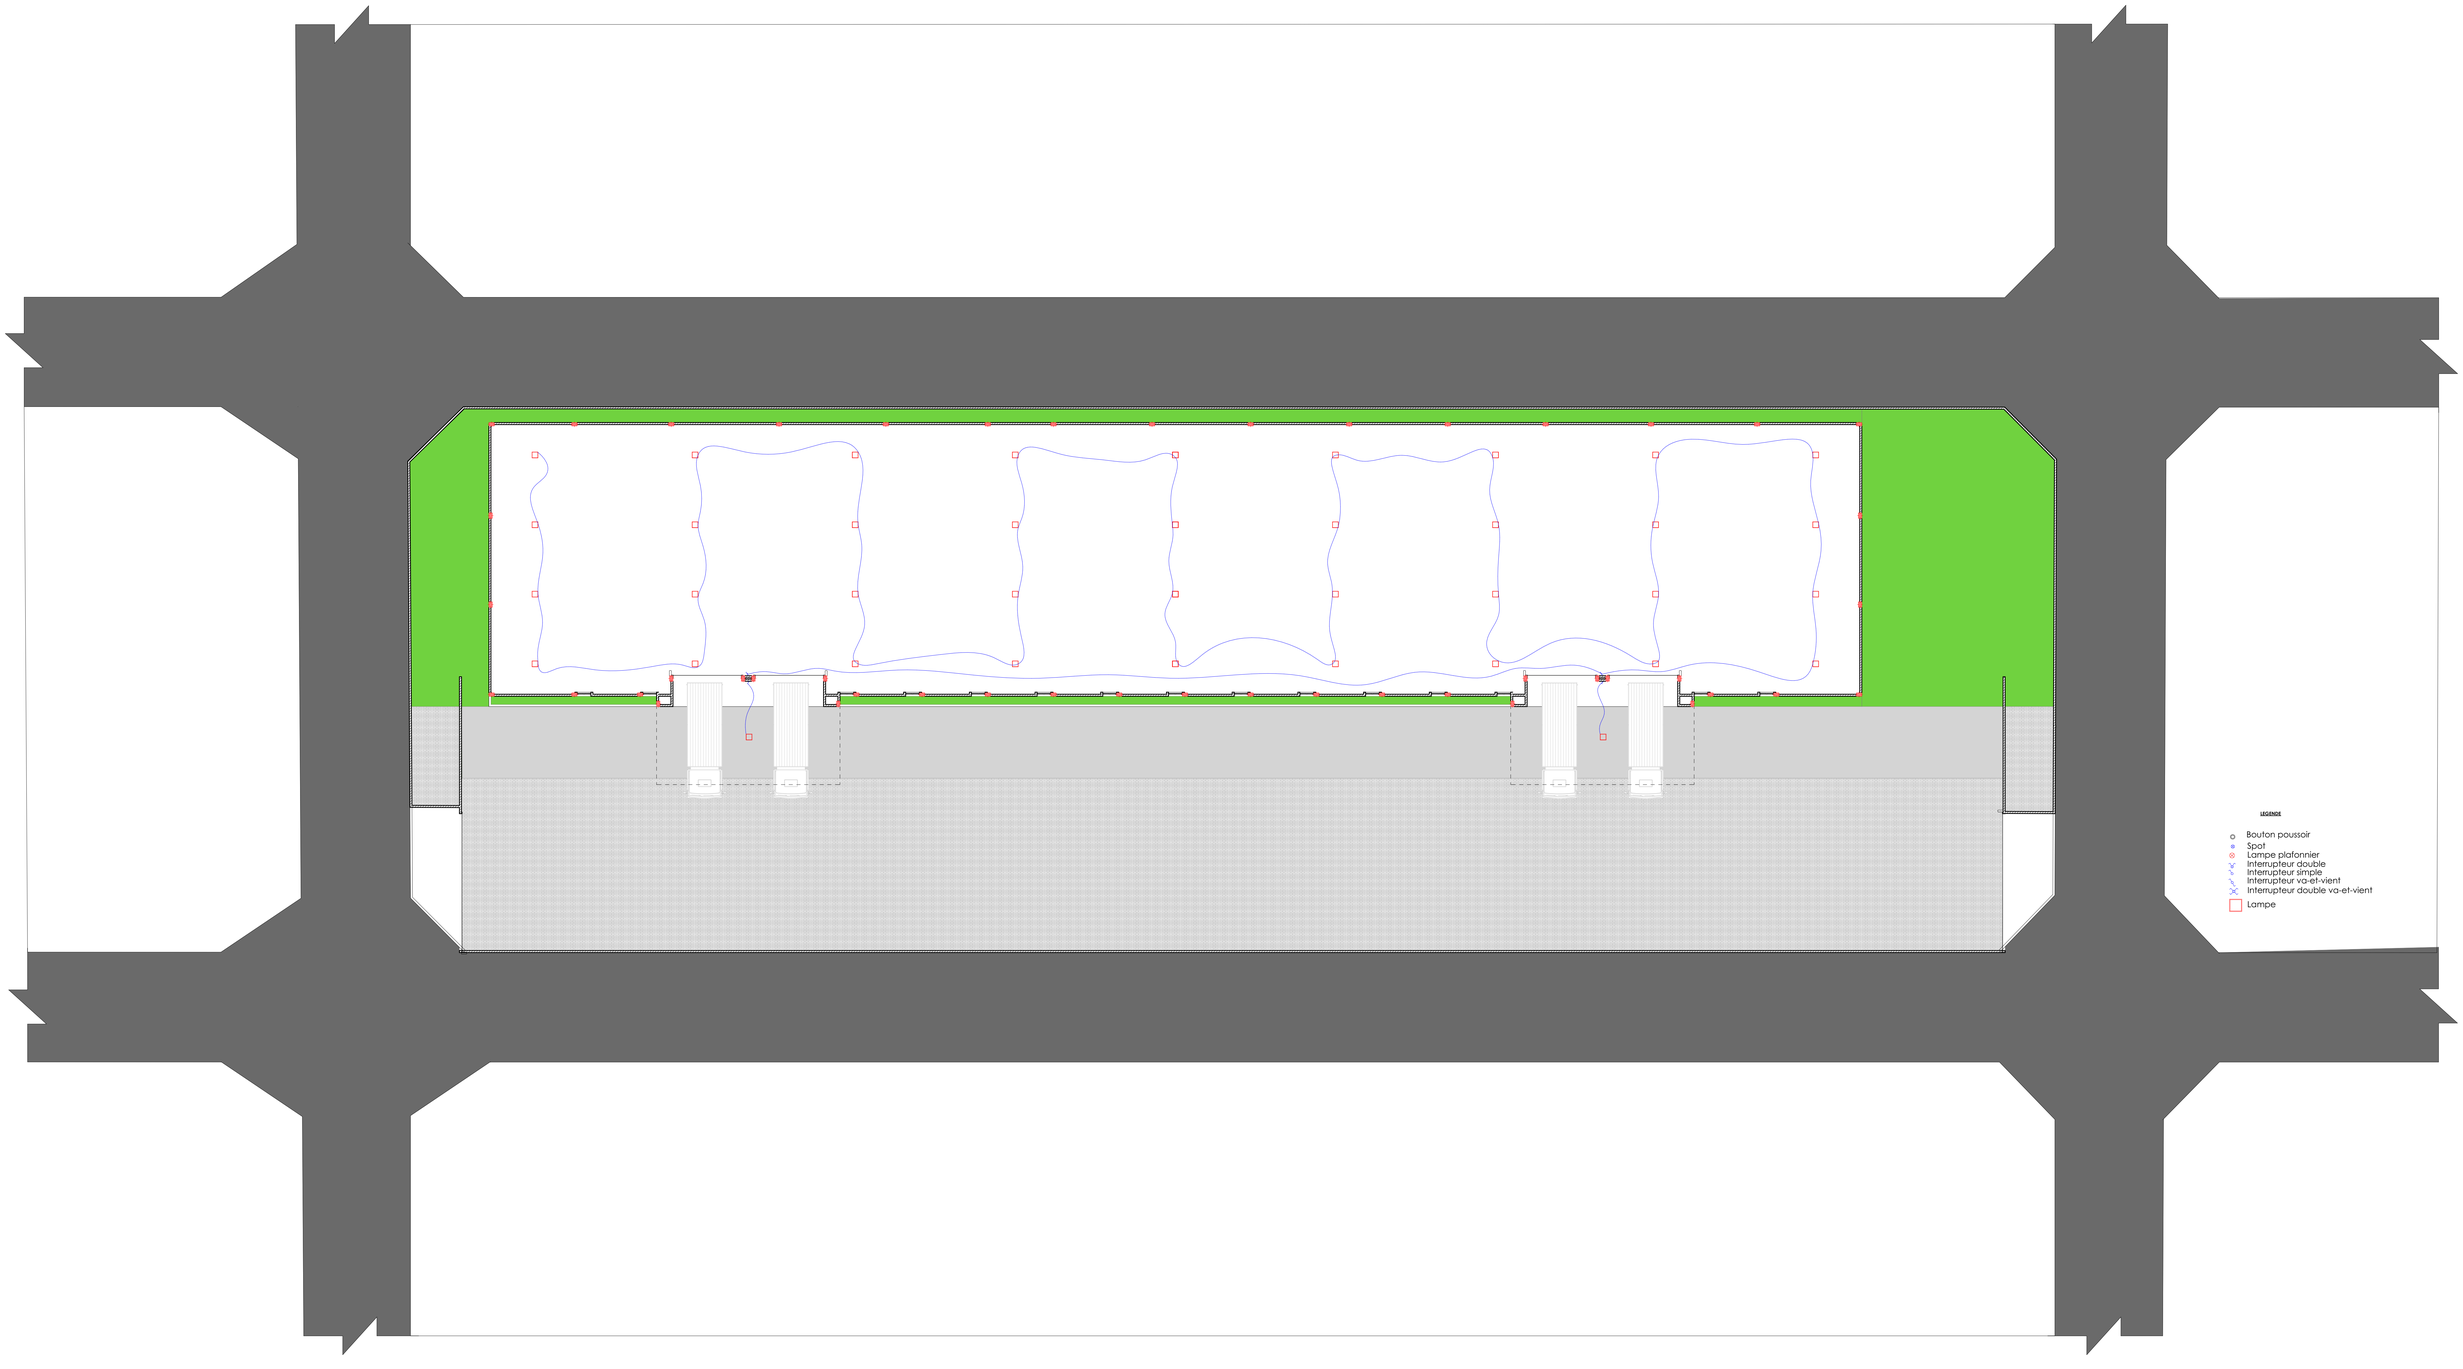

PROJET DE CONSTRUCTION D'UNE INDUSTRIE A COYAH

MAITRE D'OUVRAGE: PAPEL INDUSTRIES

MAITRE D'OEUVRE: BETCON AI

CONTACT: 625 728 627


PLAN D'ECLAIRAGE

DATE:19/12/25

ECHELLE :1/100


FORMAT :A0

BETCOM AI

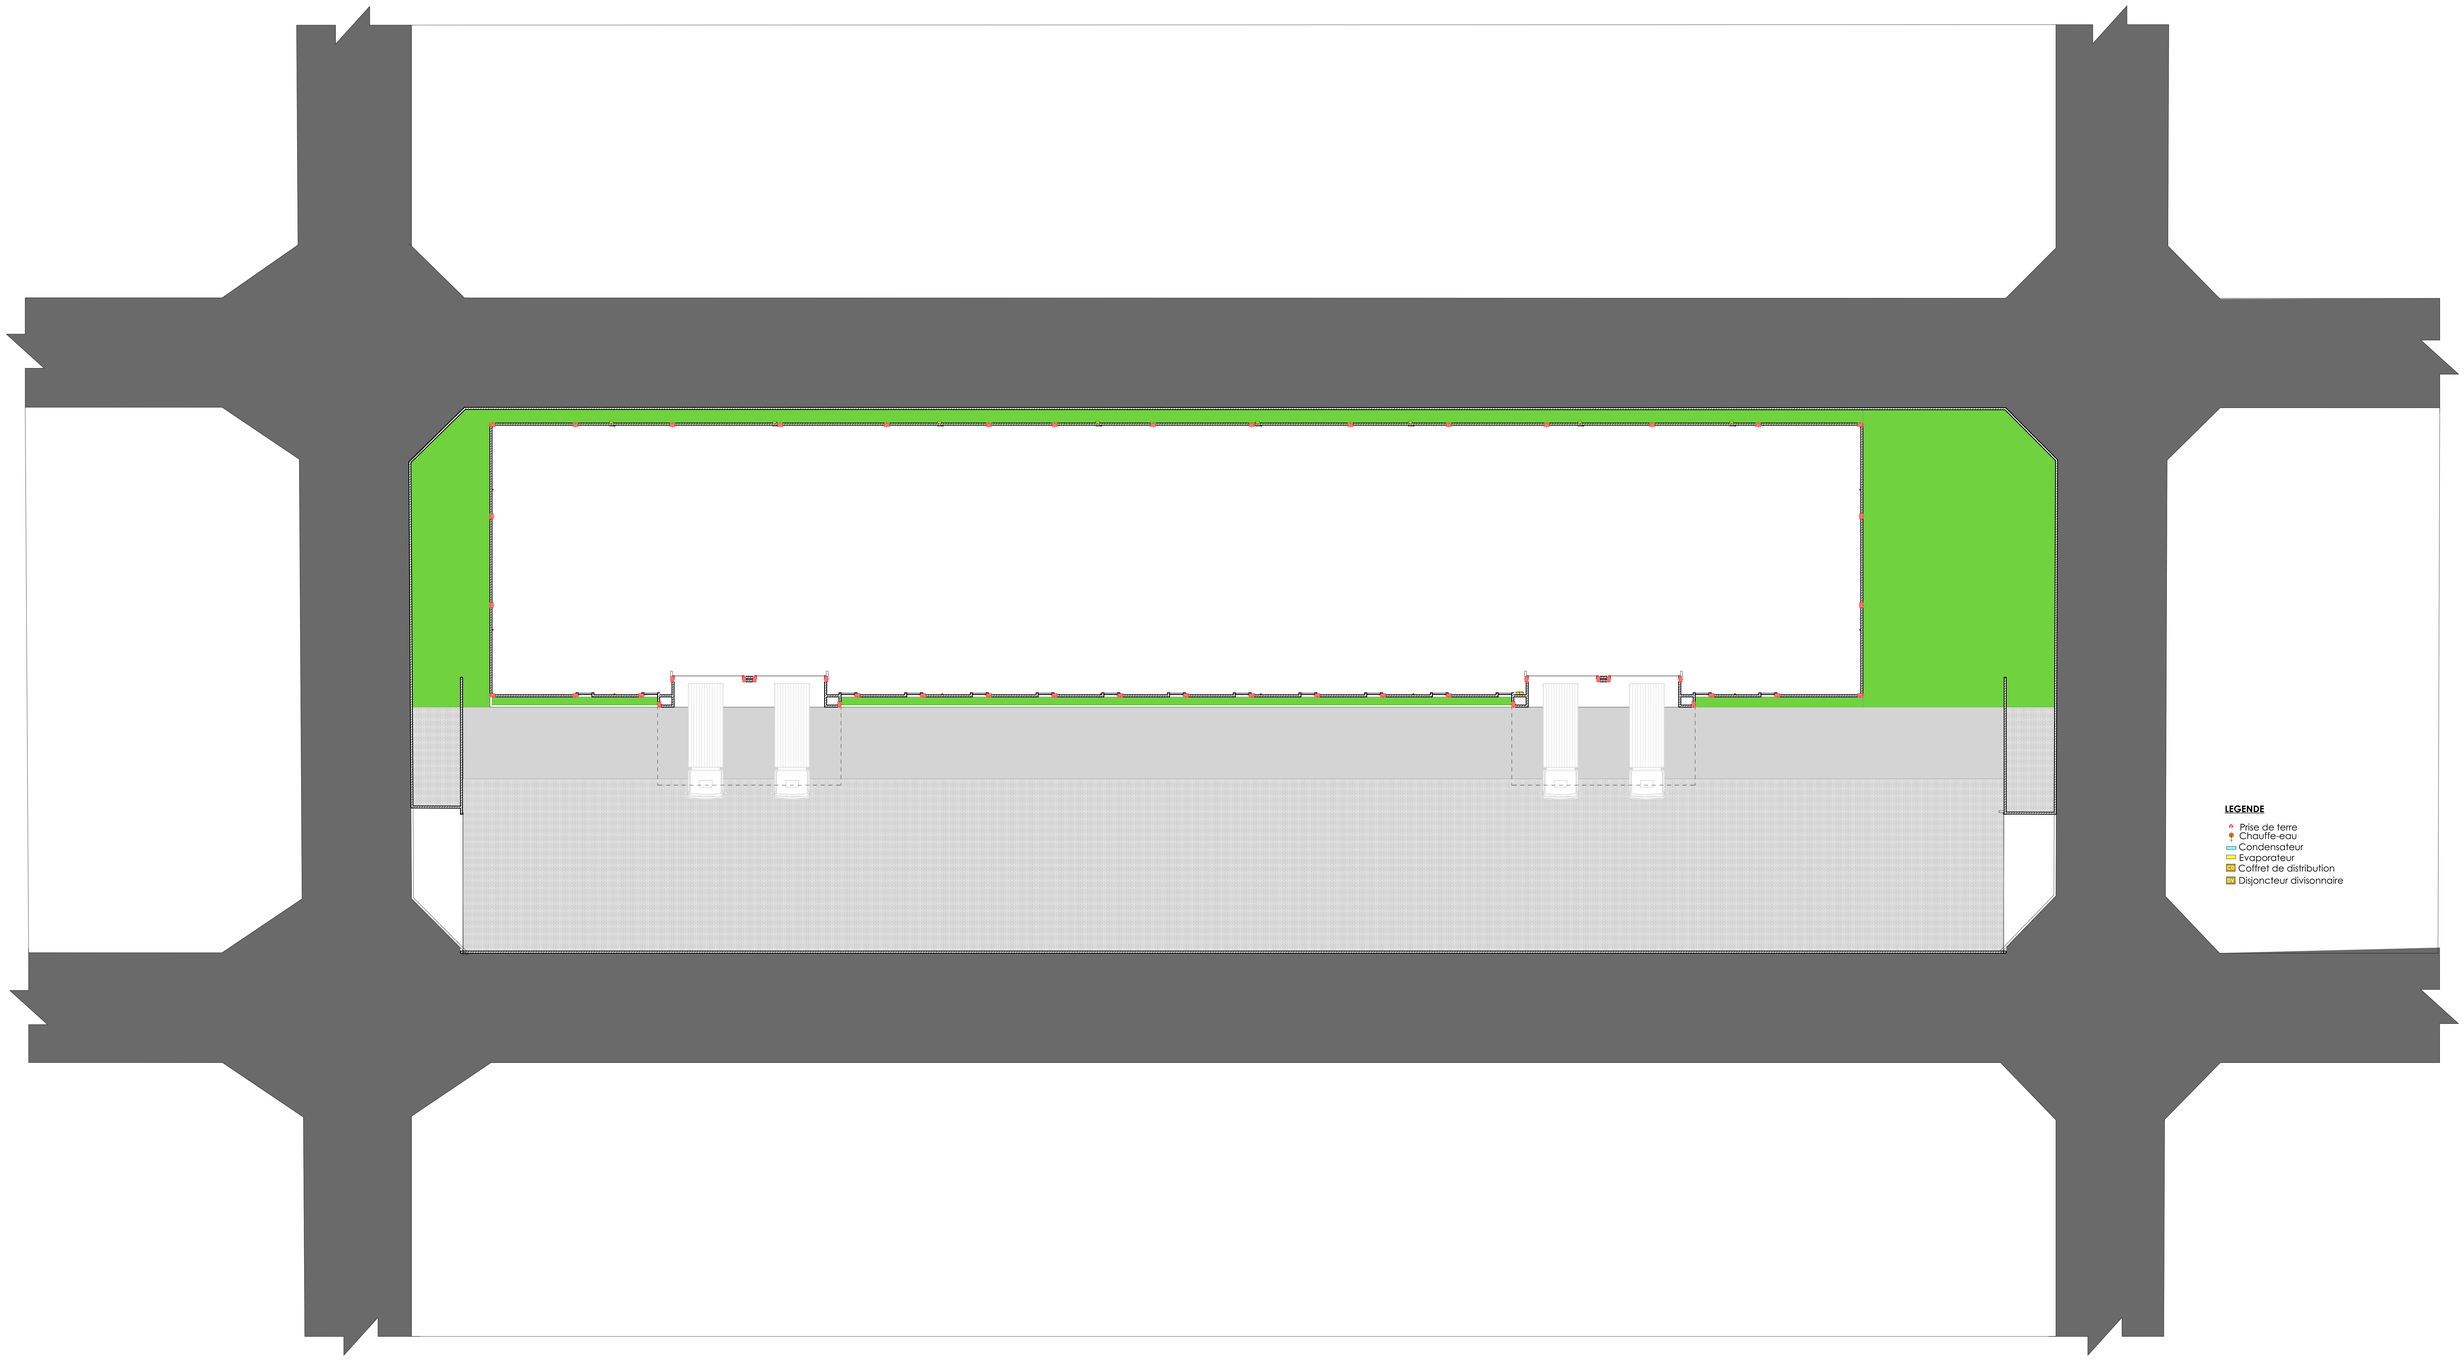

PROJET DE CONSTRUCTION D'UNE INDUSTRIE A COYAH
MAITRE D'OUVRAGE: PAPEL INDUSTRIES
MAITRE D'OEUVRE: BETCON AI
CONTACT: 625 728 627

PLAN D'ALIMENTATION
DATE:19/12/25
ECHELLE :1/100
FORMAT :A0

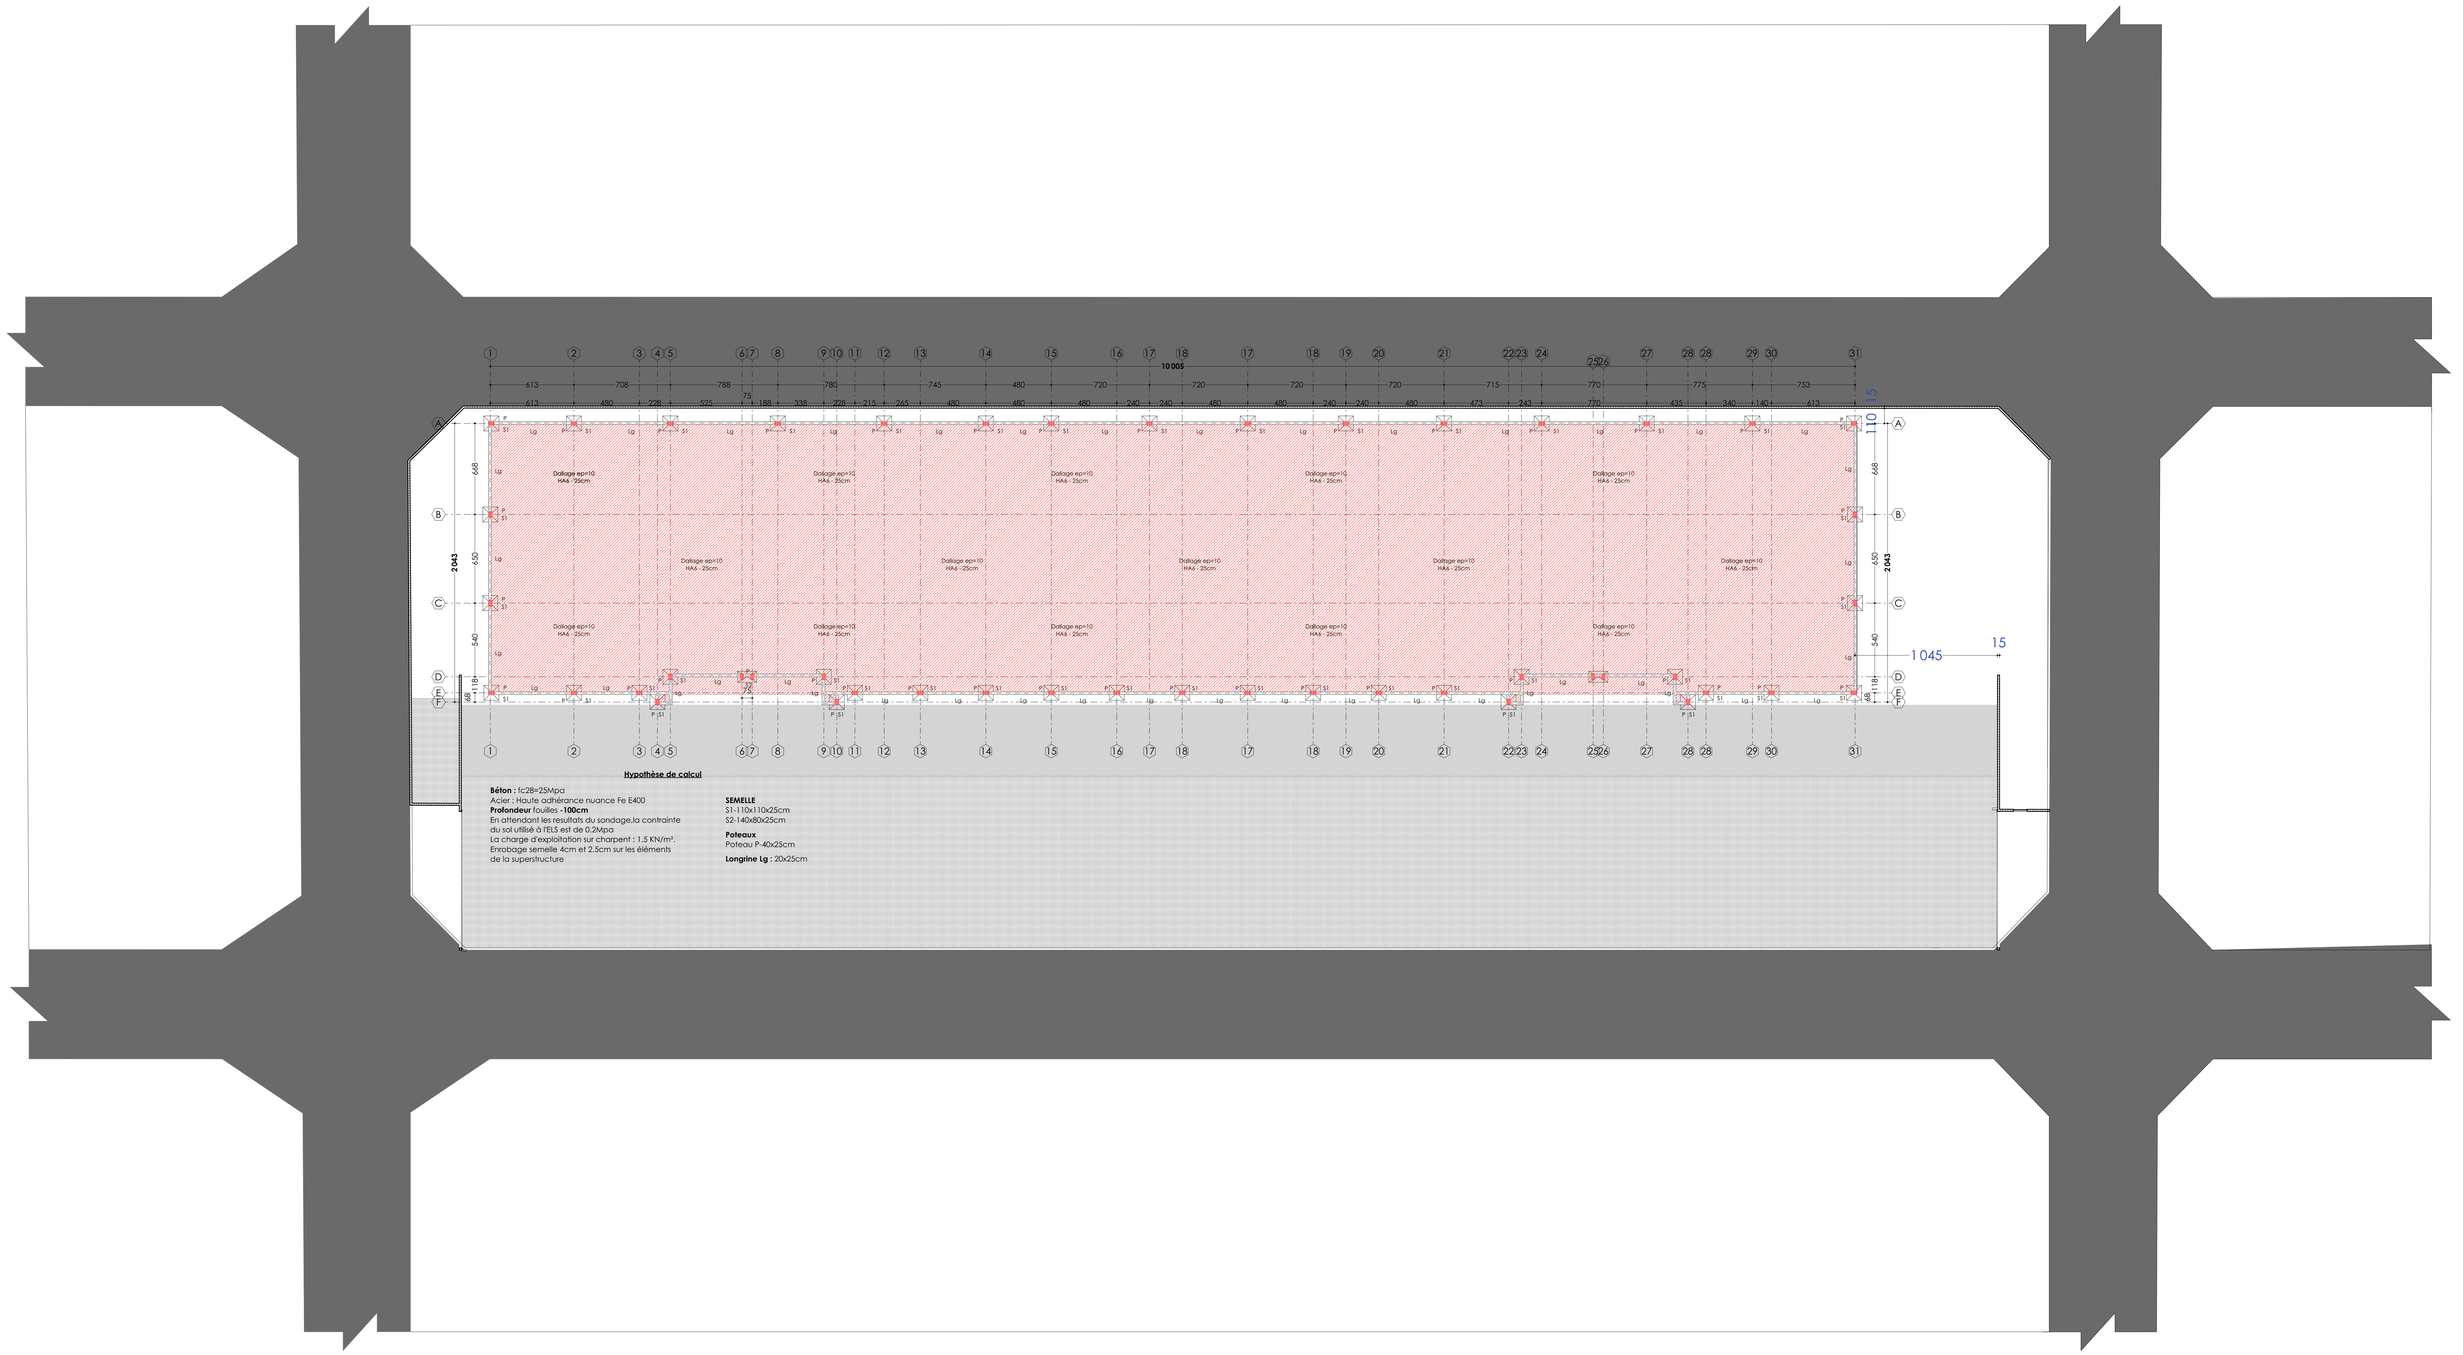

PROJET DE CONSTRUCTION D'UNE INDUSTRIE A COYAH

MAITRE D'OUVRAGE: PAPEL INDUSTRIES

MAITRE D'OEUVRE: BETCON AI


CONTACT: 625 728 627

PLAN D'IMPLANTATION

DATE:19/12/25

ECHELLE :1/100

FORMAT :A0

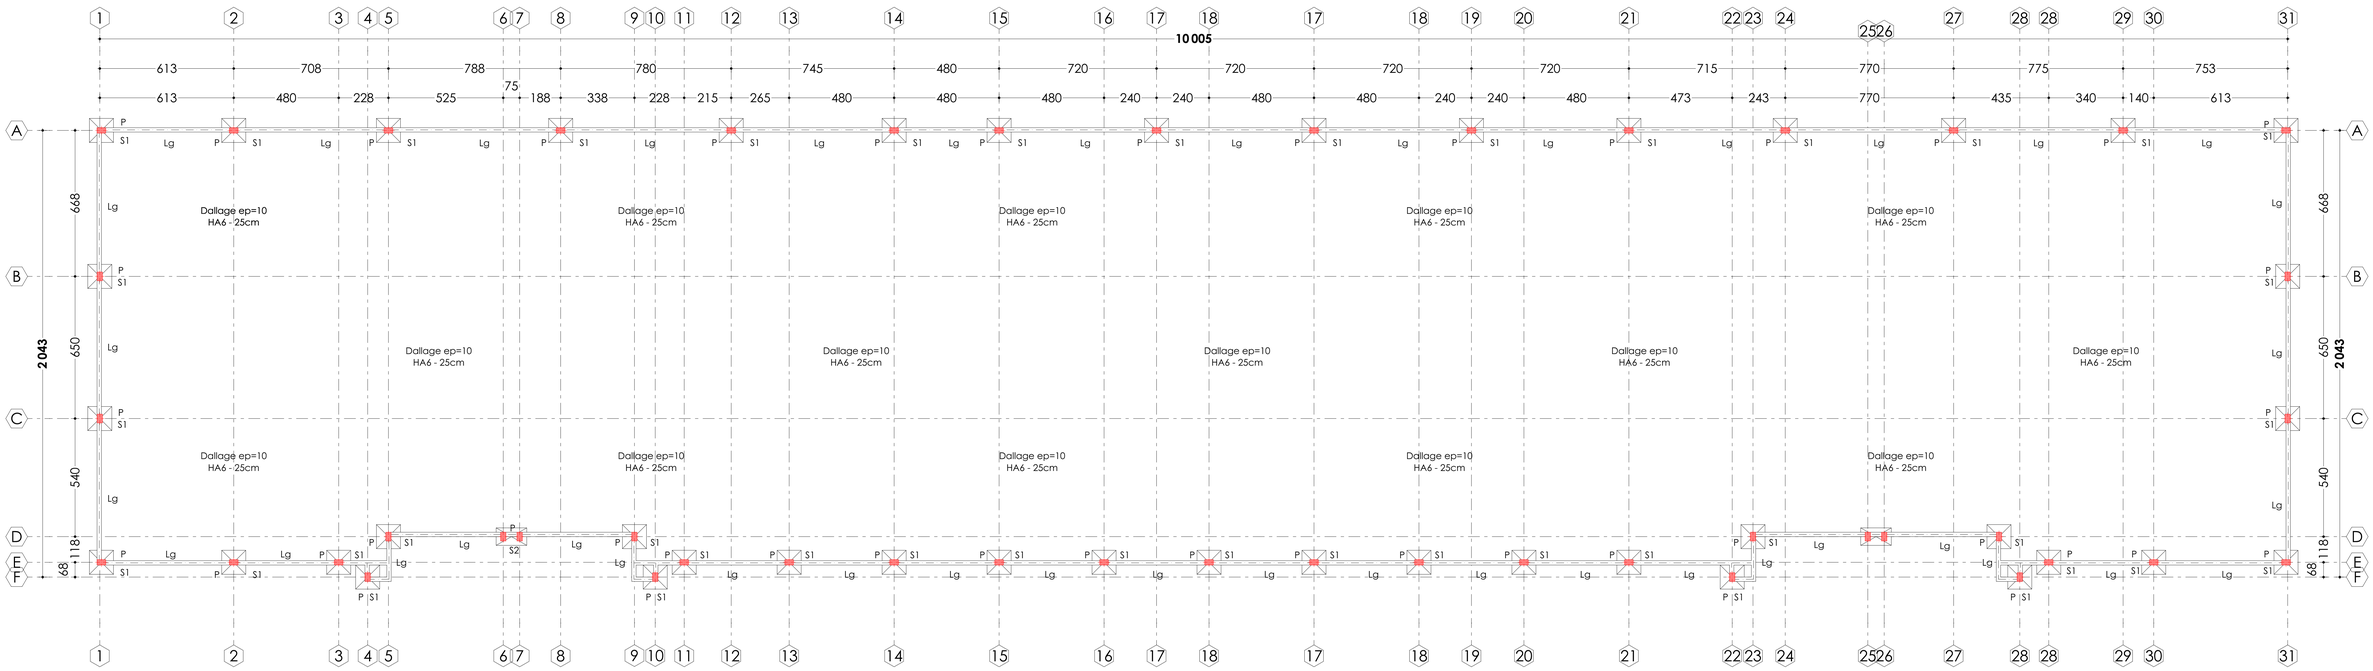

Hypothèse de calcul

Béton : fc28=25Mpa
Acier : Haute adhérance nuance Fe E400
Profondeur fouilles **-100cm**
En attendant les resultats du sondage,la contrainte du sol utilisé à l'ELS est de 0.2Mpa
La charge d'exploitation sur charpent : 1.5 KN/m².
Enrobage semelle 4cm et 2.5cm sur les éléments de la superstructure

SEMELLE
S1-110x110x25cm
S2-140x80x25cm


Poteaux
Poteau P-40x25cm


Longrine Lg : 20x25cm


PROJET DE CONSTRUCTION D'UNE INDUSTRIE A COYAH
MAITRE D'OUVRAGE: PAPEL INDUSTRIES
MAITRE D'OEUVRE: BETCON AI
CONTACT: 625 728 627


COFFRAGE FONDATION
DATE:19/12/25
ECHELLE :1/100
FORMAT :A0

SEMELLE 1

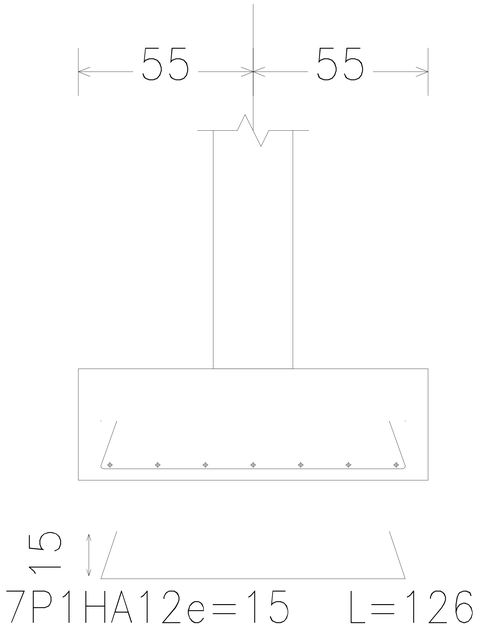

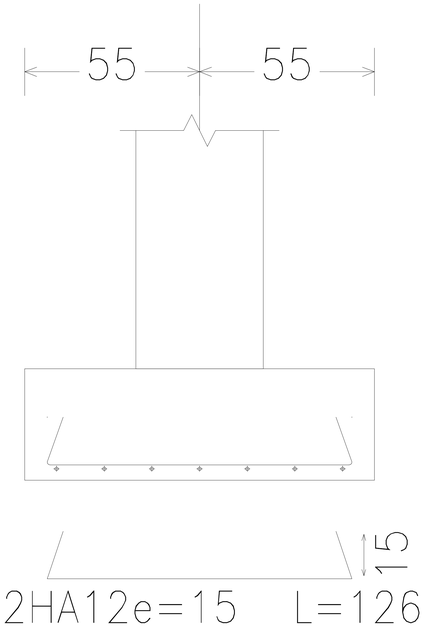

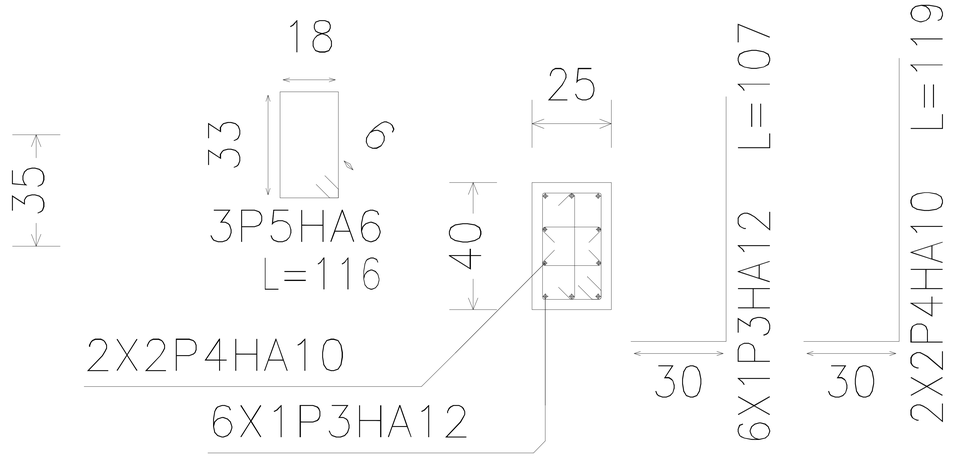

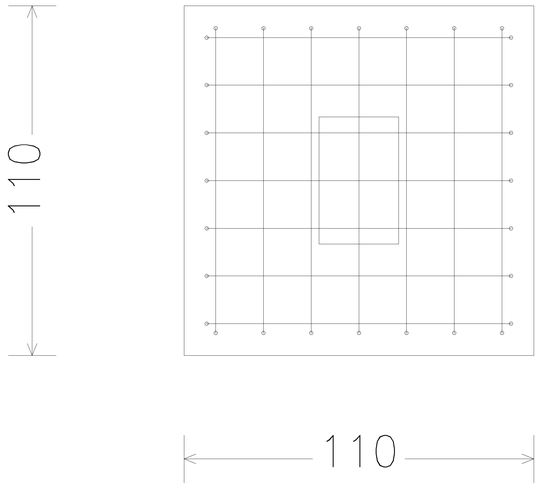



Élément	Pos.	Diam.	No.	Long. (cm)	Total (cm)	Fe E500 (kg)
S1	1	HA12	7	126	882	7.8
	2	HA12	7	126	882	7.8
	3	HA12	6	107	642	5.7
	4	HA10	4	119	476	2.9
	5	HA6	3	116	348	0.8
					Total+10%:	27.5
					HA6:	0.9
					HA10:	3.2
					HA12:	23.4
					Total:	27.5


PROJET DE CONSTRUCTION D'UNE INDUSTRIE A COYAH
MAITRE D'OUVRAGE: PAPEL INDUSTRIES
MAITRE D'OEUVRE: BETCON AI
CONTACT: 625 728 627


DETAIL : SEMELLE 1
DATE:19/12/25
ECHELLE :1/100
FORMAT :A0

SEMELLE 2

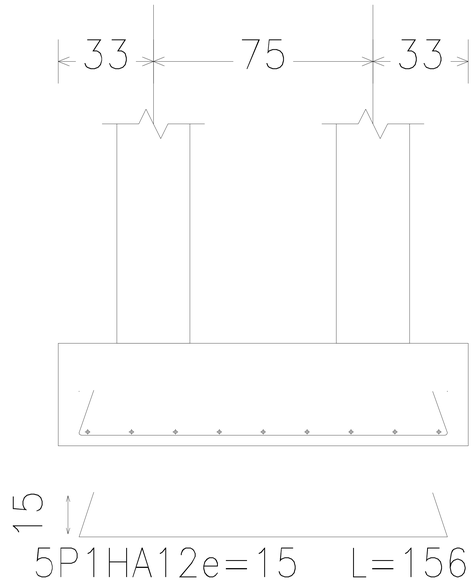

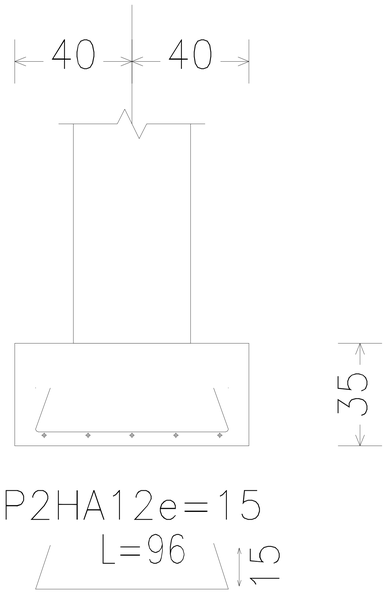

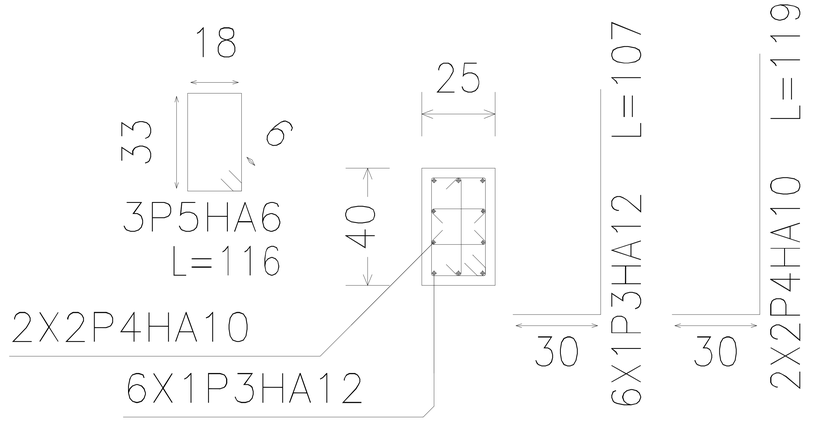


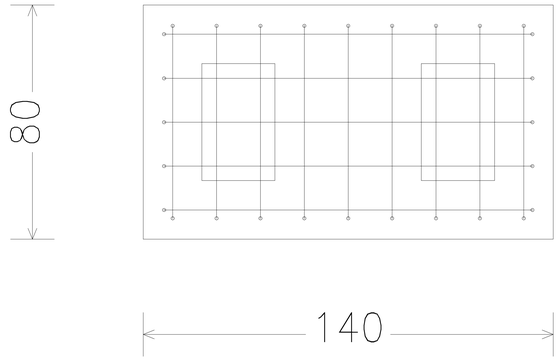

Élément	Pos.	Diam.	No.	Long. (cm)	Total (cm)	Fe E500 (kg)
S2	1	HA12	5	156	780	6.9
	2	HA12	9	96	864	7.7
	3	HA12	6	107	642	5.7
	4	HA10	4	119	476	2.9
	5	HA6	3	116	348	0.8
	6	HA12	6	107	642	5.7
	7	HA10	4	119	476	2.9
	8	HA6	3	116	348	0.8
					Total+10%:	36.7
					HA6:	1.7
					HA10:	6.4
					HA12:	28.6
					Total:	36.7


PROJET DE CONSTRUCTION D'UNE INDUSTRIE A COYAH
MAITRE D'OUVRAGE: PAPEL INDUSTRIES
MAITRE D'OEUVRE: BETCON AI
CONTACT: 625 728 627


DETAIL : SEMELLE 2
DATE:19/12/25
ECHELLE :1/100
FORMAT :A0

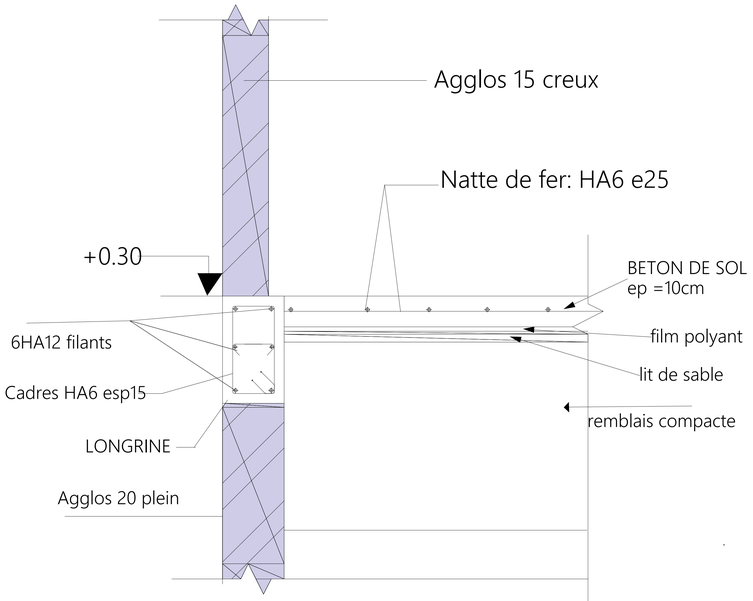

LONGRINE ET LA


FONDATION

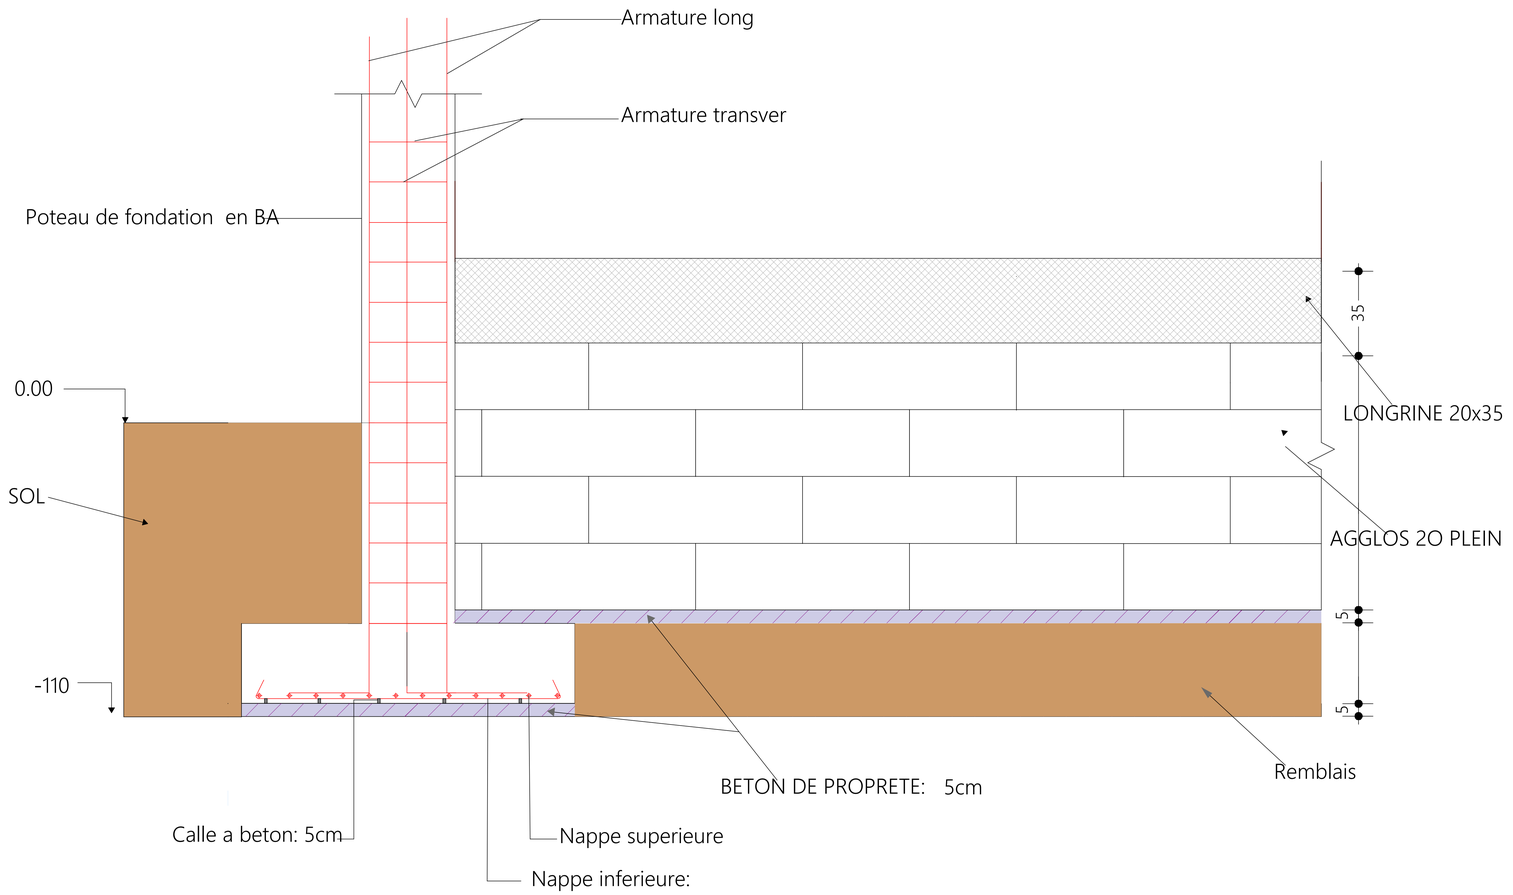

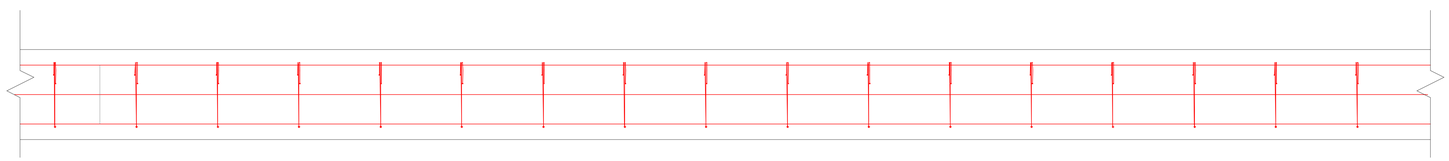

6HA12


LONGRINE

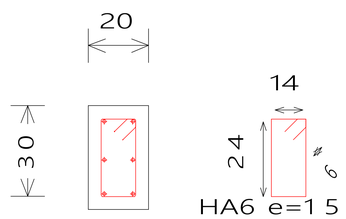


PROJET DE CONSTRUCTION D'UNE INDUSTRIE A COYAH
MAITRE D'OUVRAGE: PAPEL INDUSTRIES
MAITRE D'OEUVRE: BETCON AI
CONTACT: 625 728 627

DETAIL : COUPE A A SEMELLE
DATE:19/12/25
ECHELLE :1/100
FORMAT :A0

P

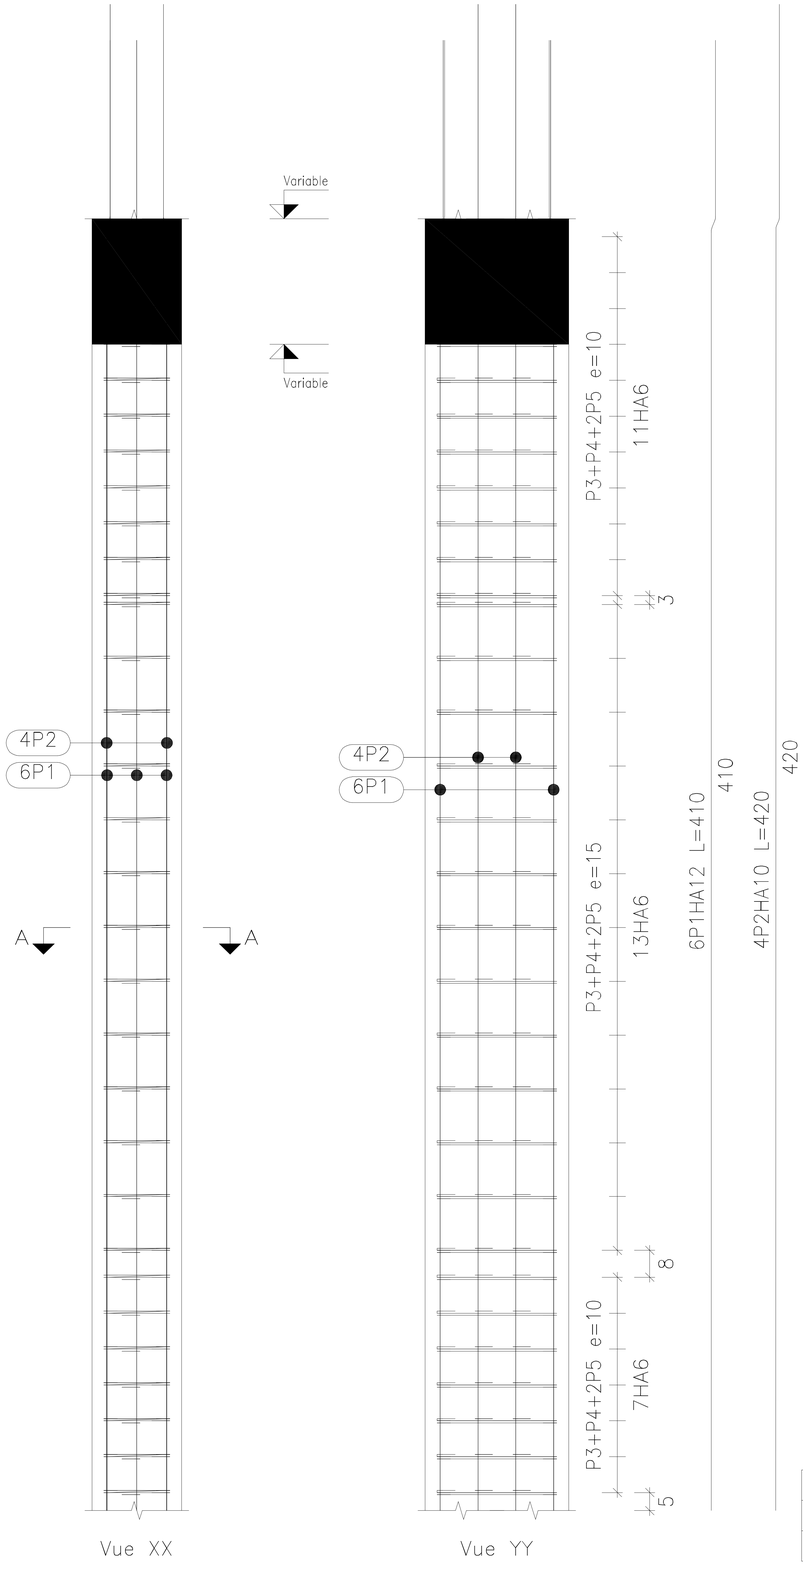


Élément	Pos.	Diam.	No.	Schéma (cm)	Long. (cm)	Total (cm)	Fe E500 (kg)
P	1	HA12	6	357 50	410	2460	21.8
	2	HA10	4	358 60	420	1680	10.4
	3	HA6	31	19 5 34	115	3565	7.9
	4	HA6	31	5 34	46	1426	3.2
	5	HA6	62	5 19	31	1922	4.3
					Total+10%:		52.4
					HA6:		17.0
					HA10:		11.4
					HA12:		24.0
					Total:		52.4

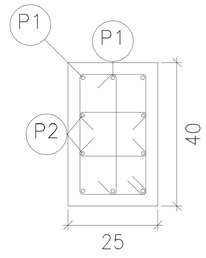


6P1HA12
4P2HA10


Section A–A

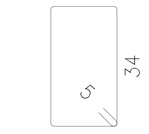

P3HA6e=15 L=115

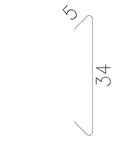

P4HA6e=15 L=46

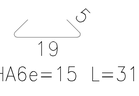

P5HA6e=15 L=31


Acier: Fe E500 (52.3 kg). Ratio: 132.06 kg/m3	
Béton: C25/30 (0.36 m3)	Diamètre du plus gros granulat: 15 mm
Coffrage: 4.68 m2	Enrobage géométrique: 3 cm


PROJET DE CONSTRUCTION D'UNE INDUSTRIE A COYAH
MAITRE D'OUVRAGE: PAPEL INDUSTRIES
MAITRE D'OEUVRE: BETCON AI
CONTACT: 625 728 627

DETAIL : POTEAUX
DATE:19/12/25
ECHELLE :1/100
FORMAT :A0

LONGRINE

Élément	Pos.	Diam.	No.	Schéma (cm)	Long. (cm)	Total (cm)	Fe E500 (kg)
Lg	1	HA12	2	716	735	1470	13.1
	2	HA12	2	836	855	1710	15.2
	3	HA12	2	816	835	1670	14.8
	4	HA12	2	731	750	1500	13.3
	5	HA12	2	830	830	1660	14.7
	6	HA12	2	720	720	1440	12.8
	7	HA6	96	23 6 13	86	8256	18.3
				Total+10%:			112.4
					HA6:		20.1
					HA12:		92.3
					Total:		112.4

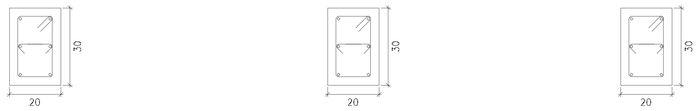

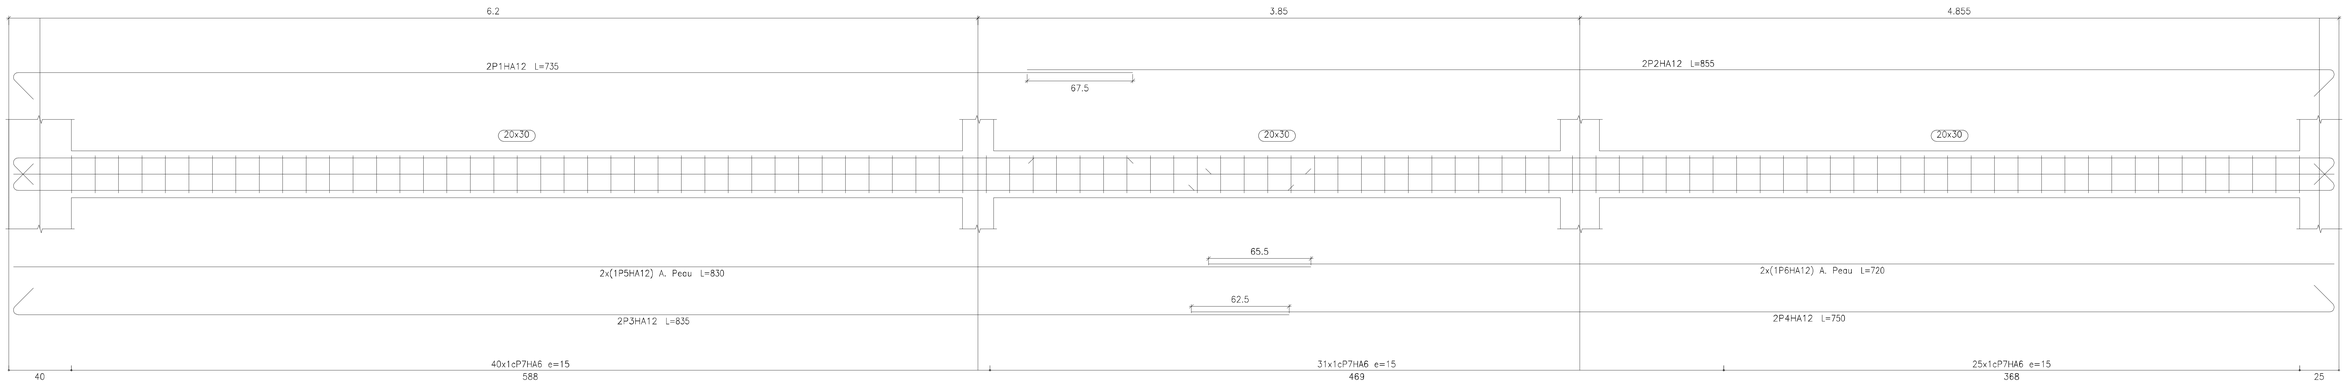

PROJET DE CONSTRUCTION D'UNE INDUSTRIE A COYAH

MAITRE D'OUVRAGE: PAPEL INDUSTRIES

MAITRE D'OEUVRE: BETCON AI

CONTACT: 625 728 627

DETAIL : LONGRINE


DATE:19/12/25

ECHELLE :1/100

FORMAT :A0

CHAINAGE

Élément	Pos.	Diam.	No.	Schéma (cm)	Long. (cm)	Total (cm)	Fe E500 (kg)
CH	1	HA12	2	735	760	1520	13.5
	2	HA12	2	815	840	1680	14.9
	3	HA12	2	725	750	1500	13.3
	4	HA12	2	825	850	1700	15.1
	5	HA12	2	220	220	440	3.9
	6	HA12	2	190	190	380	3.4
	7	HA12	2	850	850	1700	15.1
	8	HA12	2	700	700	1400	12.4
	9	HA6	96	6 / 13	106	10176	22.6
					Total+10%:		125.6
					HA6:		24.8
					HA12:		100.8
					Total:		125.6

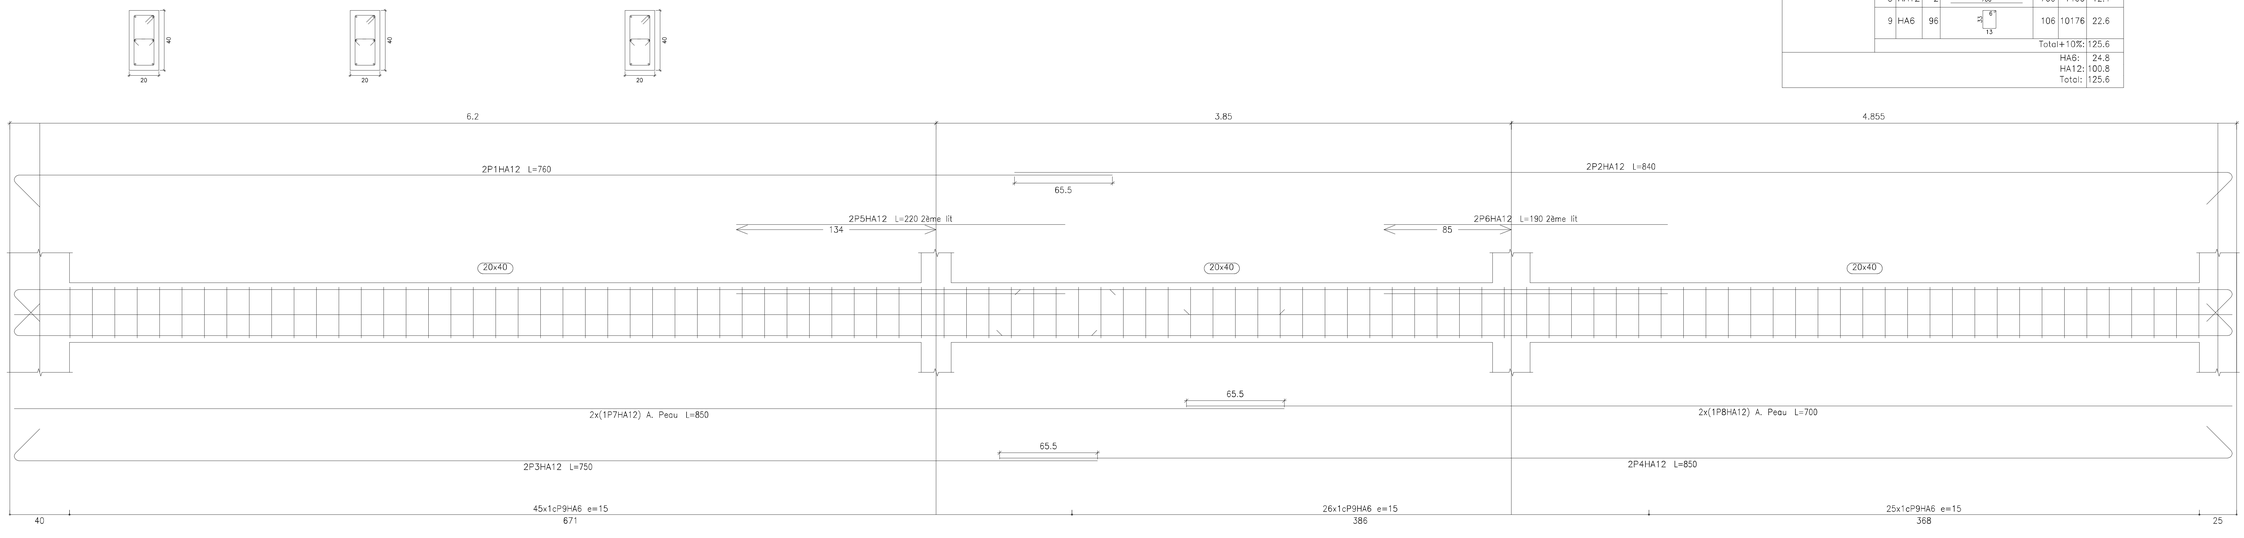

PROJET DE CONSTRUCTION D'UNE INDUSTRIE A COYAH
MAITRE D'OUVRAGE: PAPEL INDUSTRIES
MAITRE D'OEUVRE: BETCON AI
CONTACT: 625 728 627

DETAIL : CHAINAGE
DATE:19/12/25
ECHELLE :1/100
FORMAT :A0